
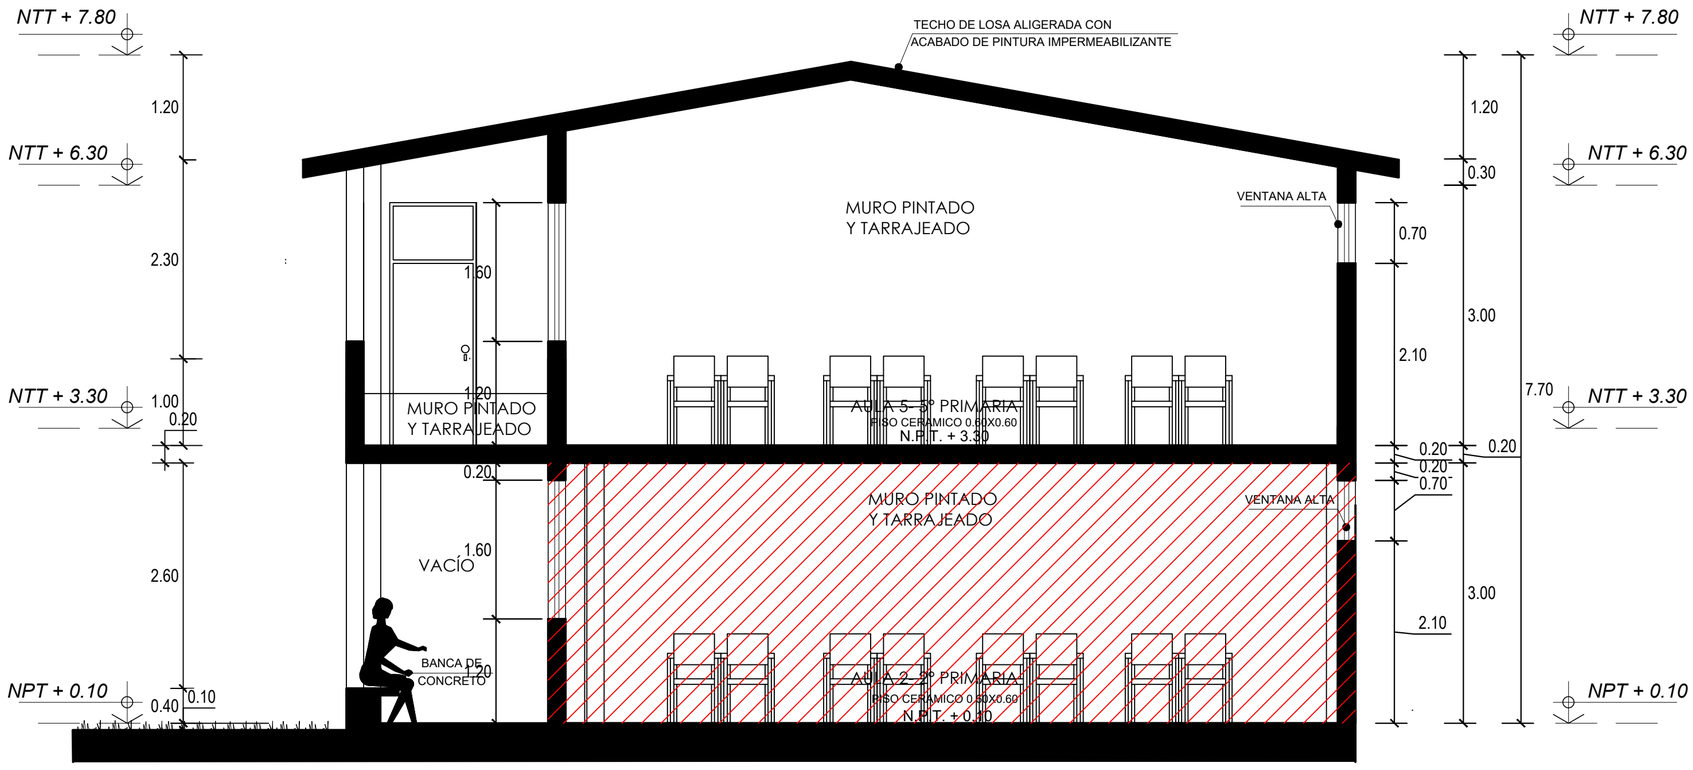



CORTE A-A

ESC. 1/50

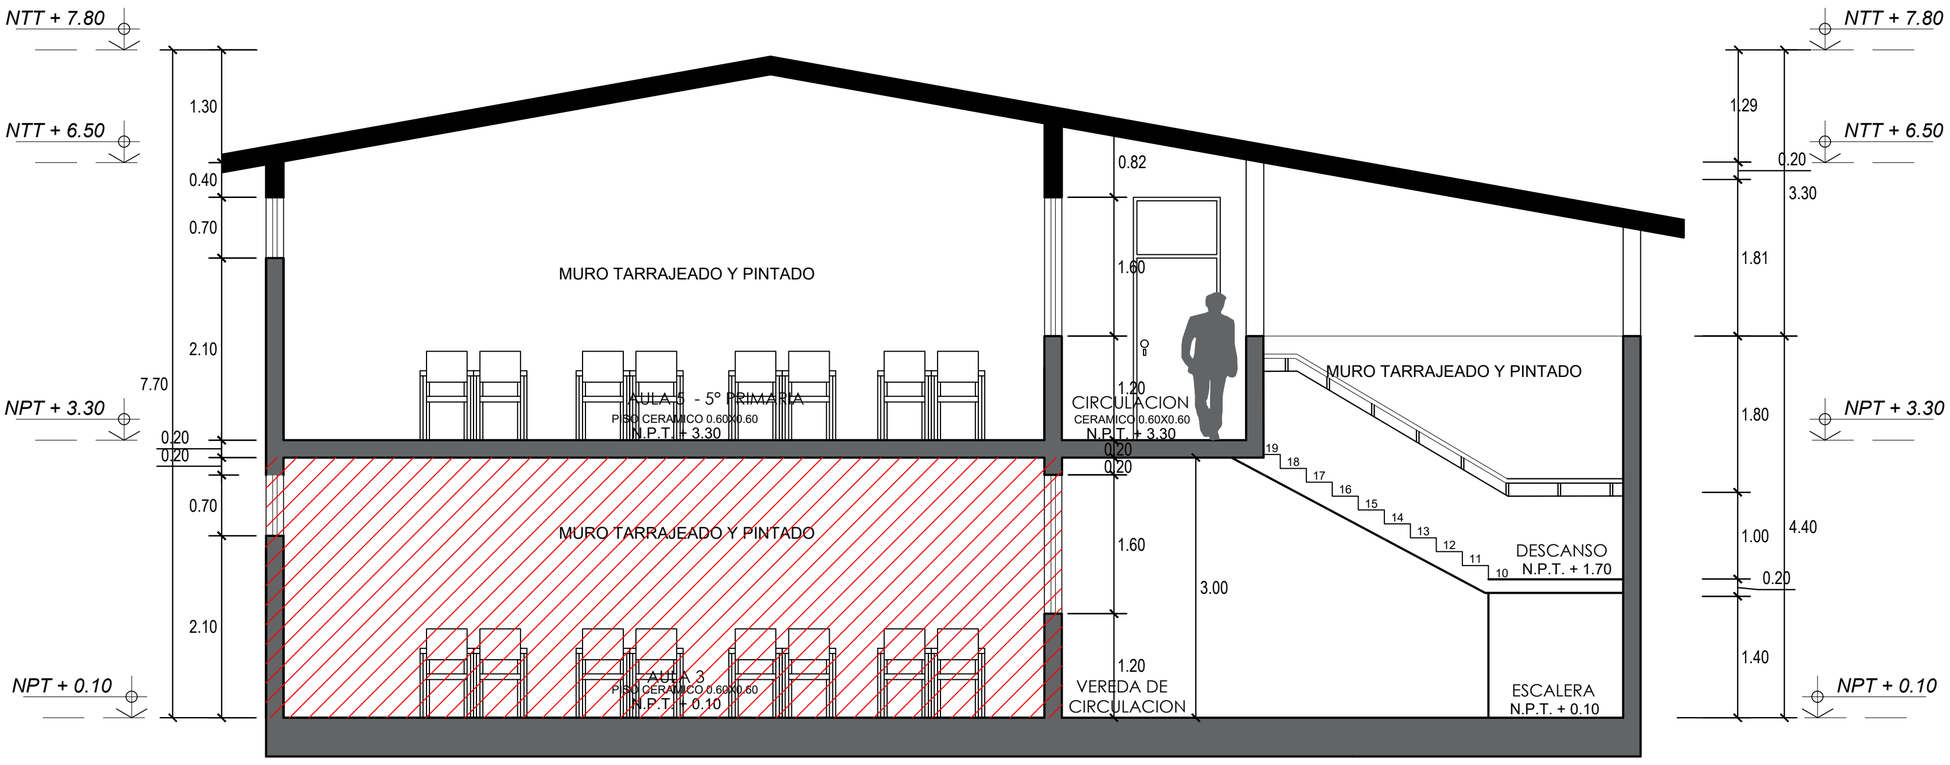

CORTE B-B

ESC. 1/50

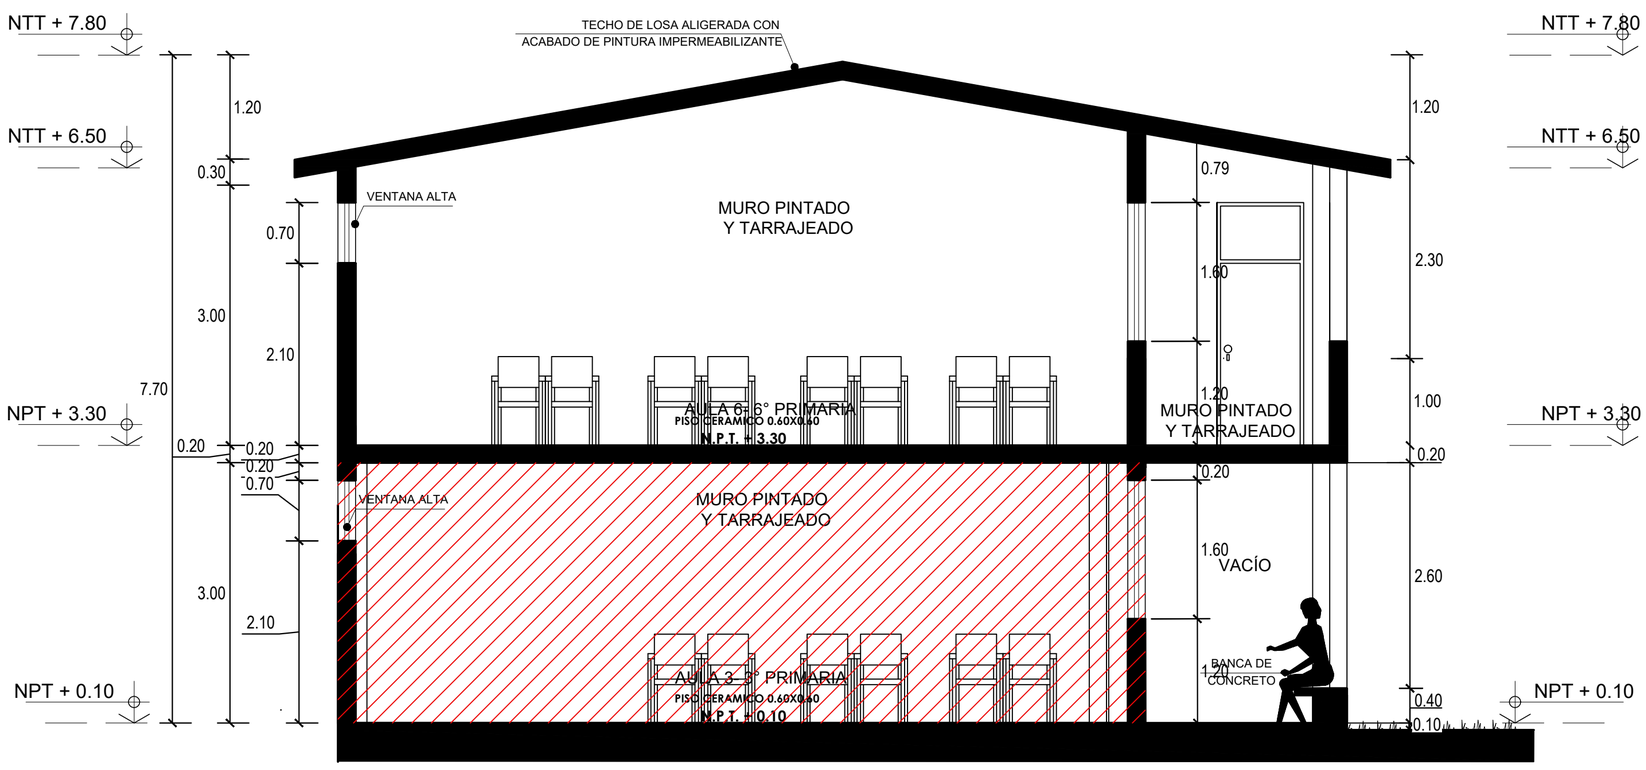

CORTE C-C

ESC. 1/50

AULAS CONSTRUÍDAS

COPRODELI

PROYECTO :	COLEGIO SISA
PLANO :	ARQUITECTURA - CORTES
UBICACIÓN :	Calle Arturo Soria N°311 distrito de San Pablo, Provincia de Bellavista, Departamento de San Martín
PROFESIONAL :	Arq. Félix Manuel Luna Nuñez CAP 25486
DIBUJO :	
ESCALA	1/50
FECHA :	NOVIEMBRE 2025
LAMINA :	A-2