
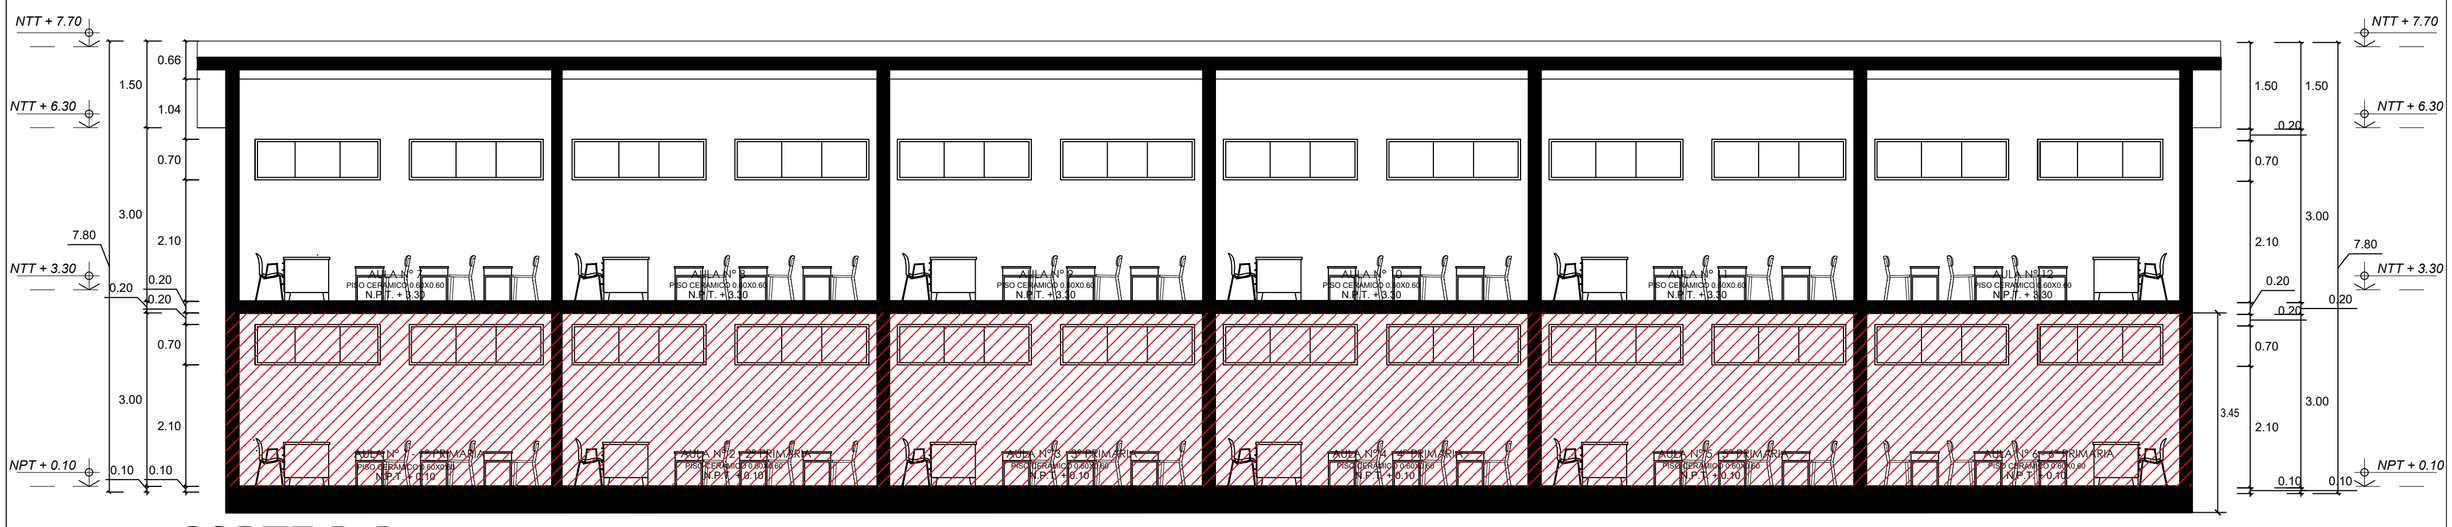



CORTE D-D

ESC. 1/75

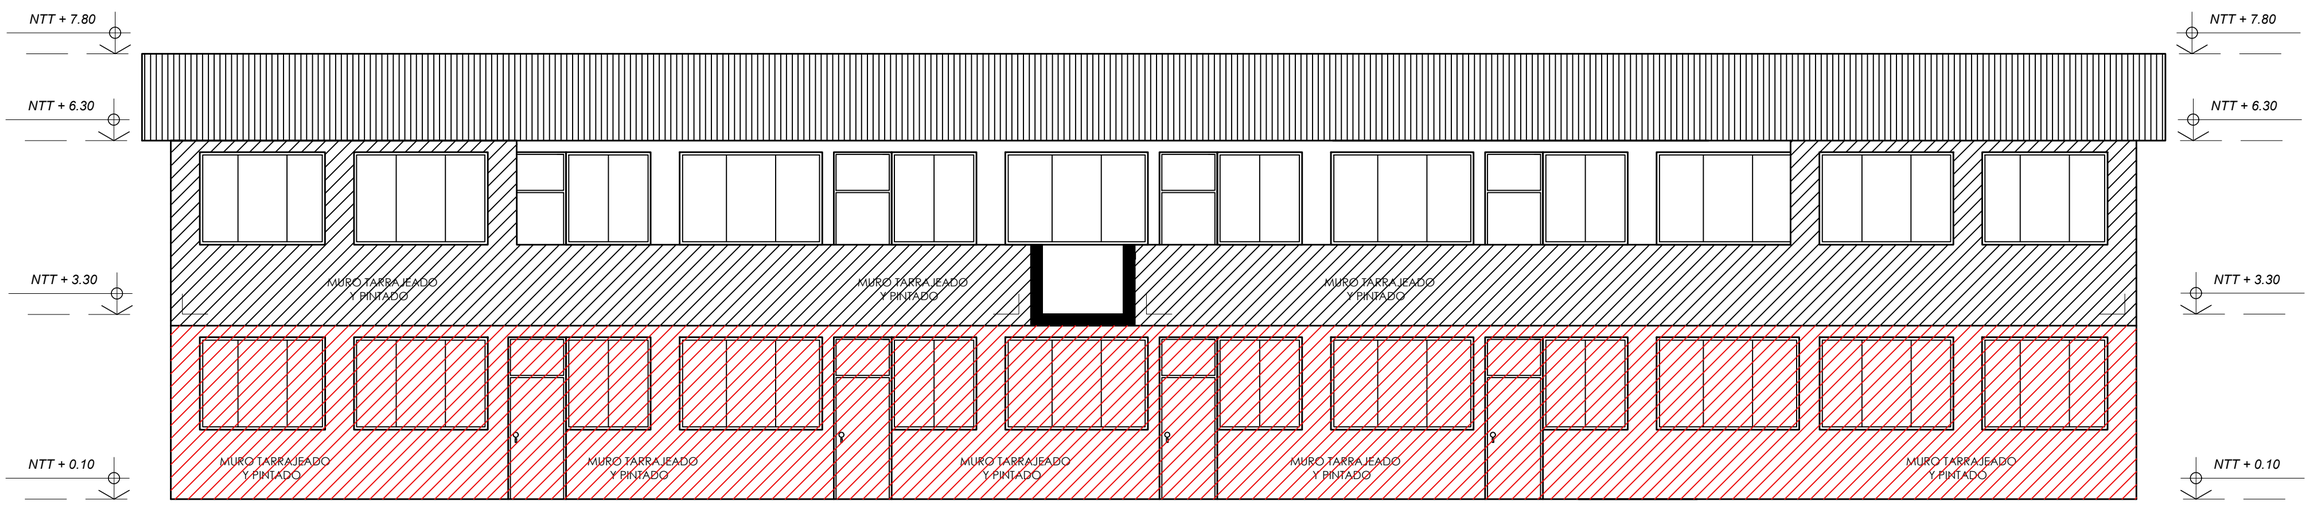


ELEVACION B-1

ESC. 1/75

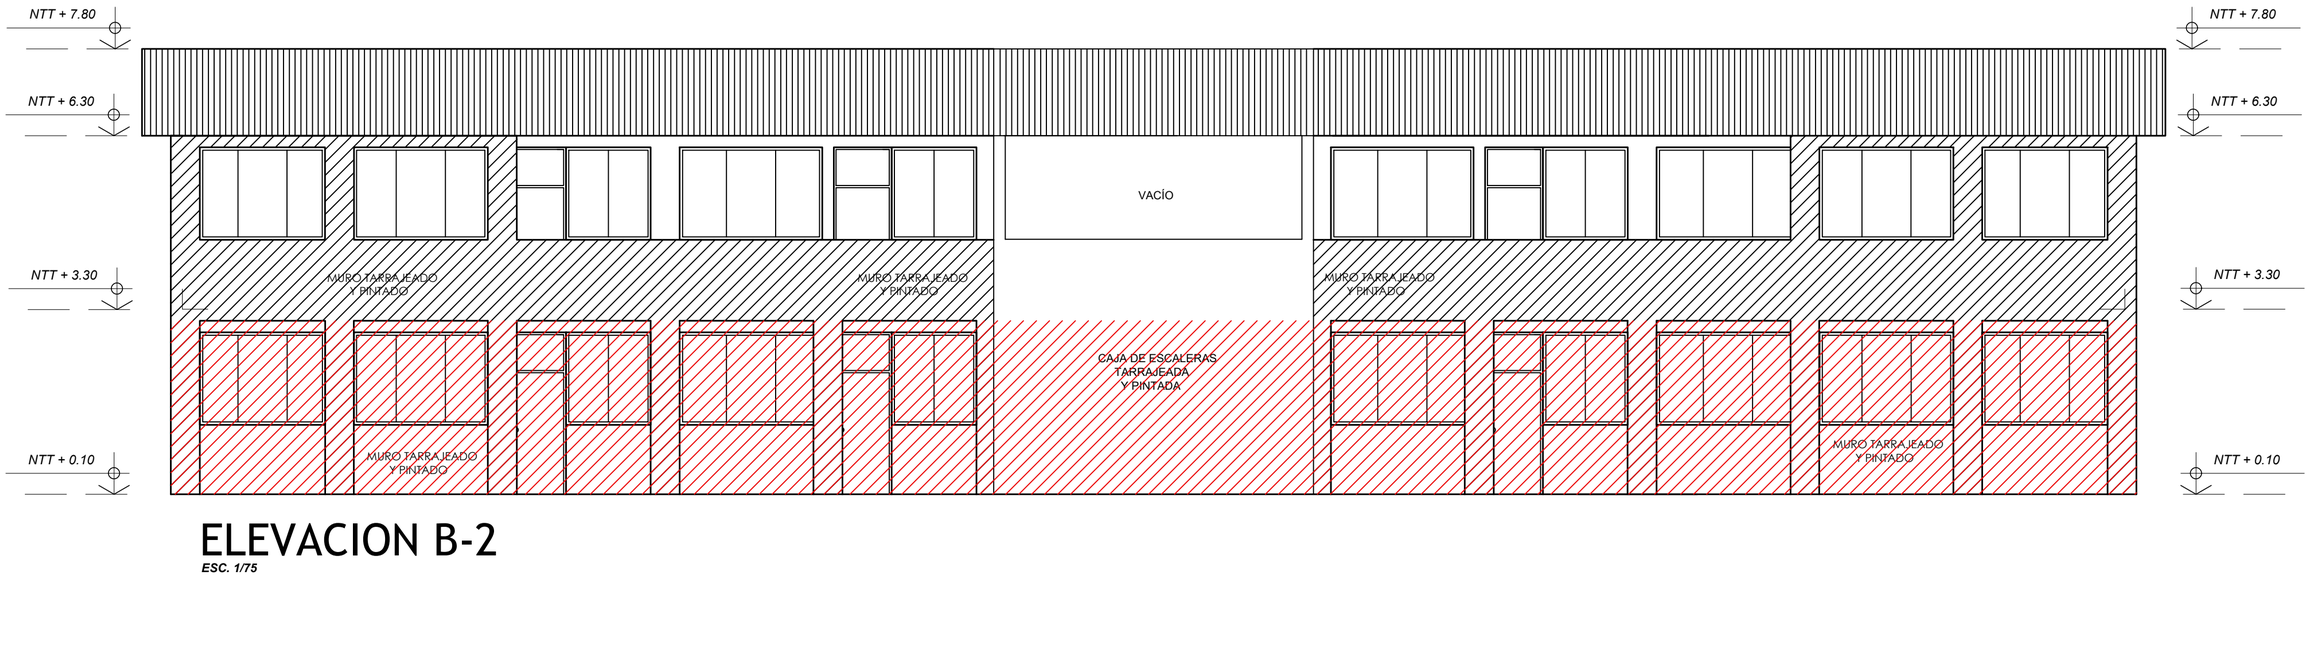

ELEVACION B-2

ESC. 1/75

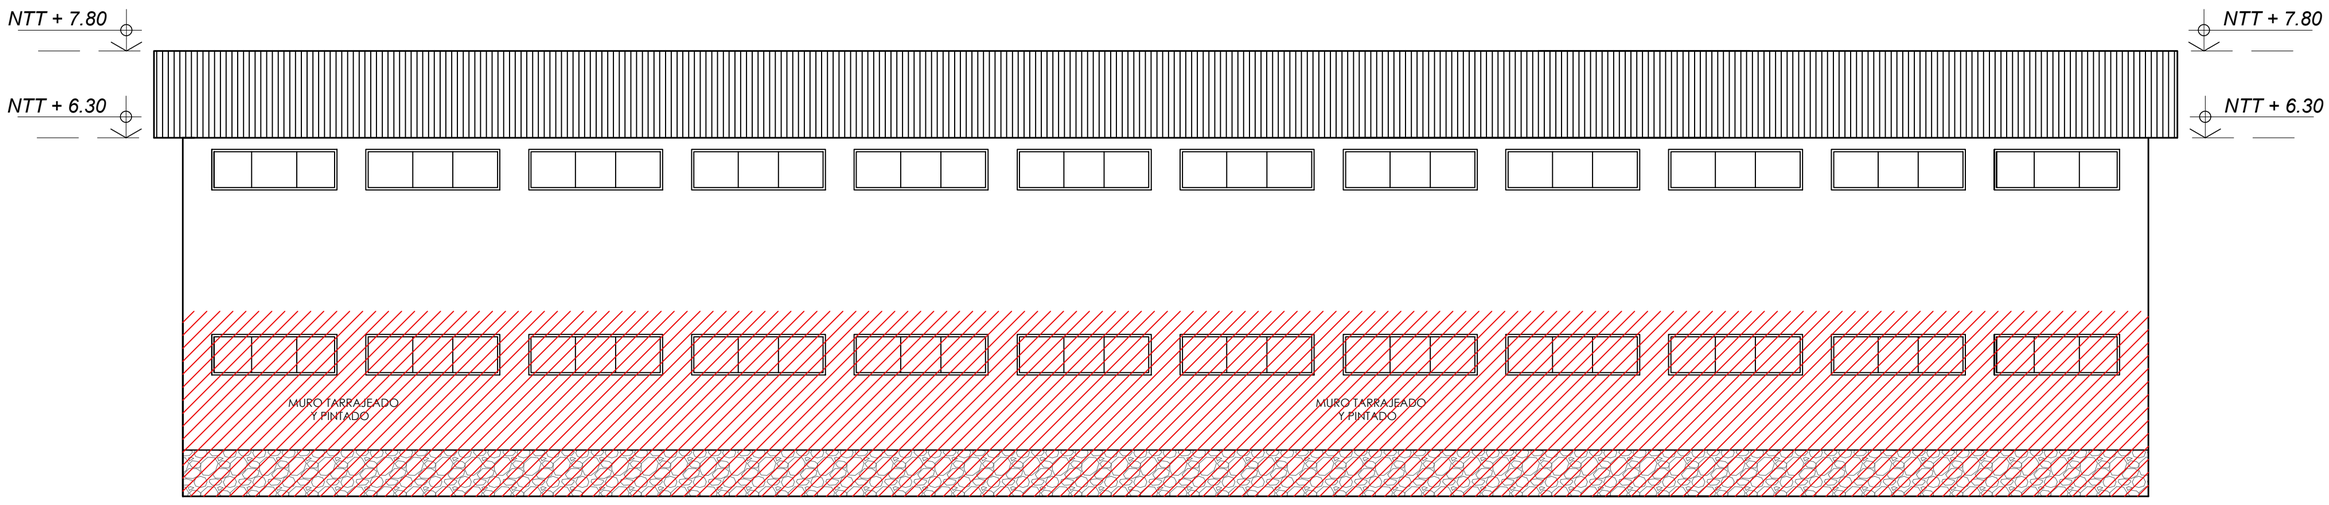

ELEVACION B-3

ESC. 1/75

AULAS CONSTRUÍDAS

COPRODELI

PROYECTO :	COLEGIO SISA
PLANO :	ARQUITECTURA - CORTES Y ELEVACIONES
UBICACIÓN :	Calle Arturo Soria Nº311 distrito de San Pablo, Provincia de Bellavista, Departamento de San Martín
PROFESIONAL :	Arq. Félix Manuel Luna Nuñez CAP 25486
DIBUJO :	
ESCALA	1/75
FECHA :	NOVIEMBRE 2025
LAMINA :	A-3