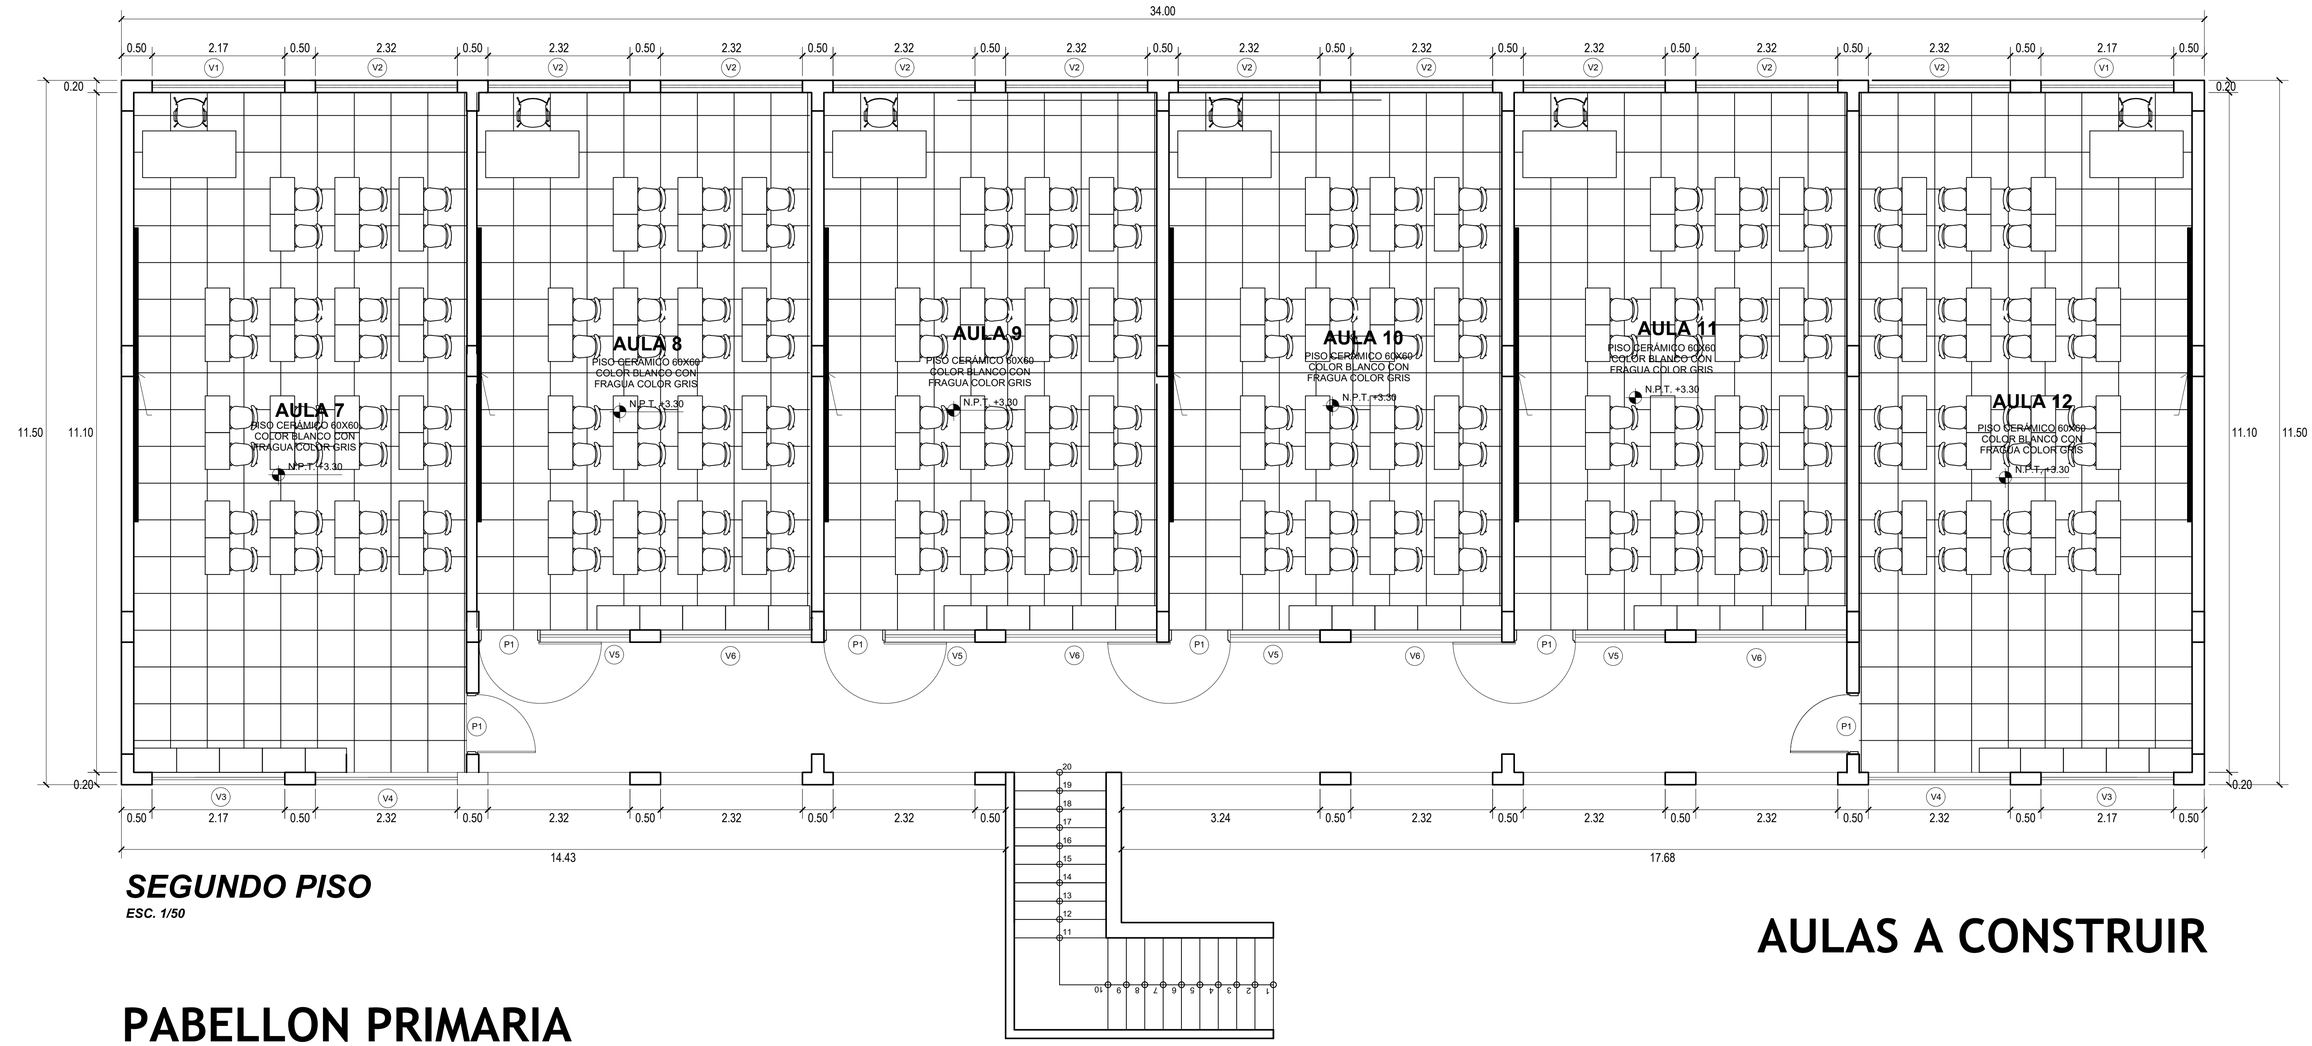


SEGUNDO PISO

ESC. 1/50

PABELLON PRIMARIA

AULAS A CONSTRUIR

CUADRO DE VANOS - VENTANAS BLOQUE 2				
TIPO	ANCHO	ALTO	ALFEIZAR	TOTAL
V–1	2.17	0.70	2.10	4
V–2	2.32	0.70	2.10	20
V–3	2.17	1.60	1.20	4
V–4	2.32	1.60	1.20	4
V–5	1.47	1.60	1.20	8
V–6	2.47	1.60	1.20	8

CUADRO DE PUERTAS-BLOQUE 2				
ITEM	ANCHO	ALTO	CARACTERISTICAS	CANTIDAD
P-1	1.00	2.10	180°	12

NOTA: La sobreluz de las puertas será 0.70 m de alto

COPRODELI

PROYECTO : COLEGIO SISA

PLANO : ARQUITECTURA - SEGUNDO NIVEL

UBICACIÓN : Calle Arturo Soria N°311 distrito de San Pablo, Provincia de Bellavista, Departamento de San Martin

PROFESIONAL : Arq. Félix Manuel Luna Nuñez CAP 25486

DIBUJO :

ESCALA 1/50

FECHA : NOVIEMBRE 2025

LAMINA : A-1