

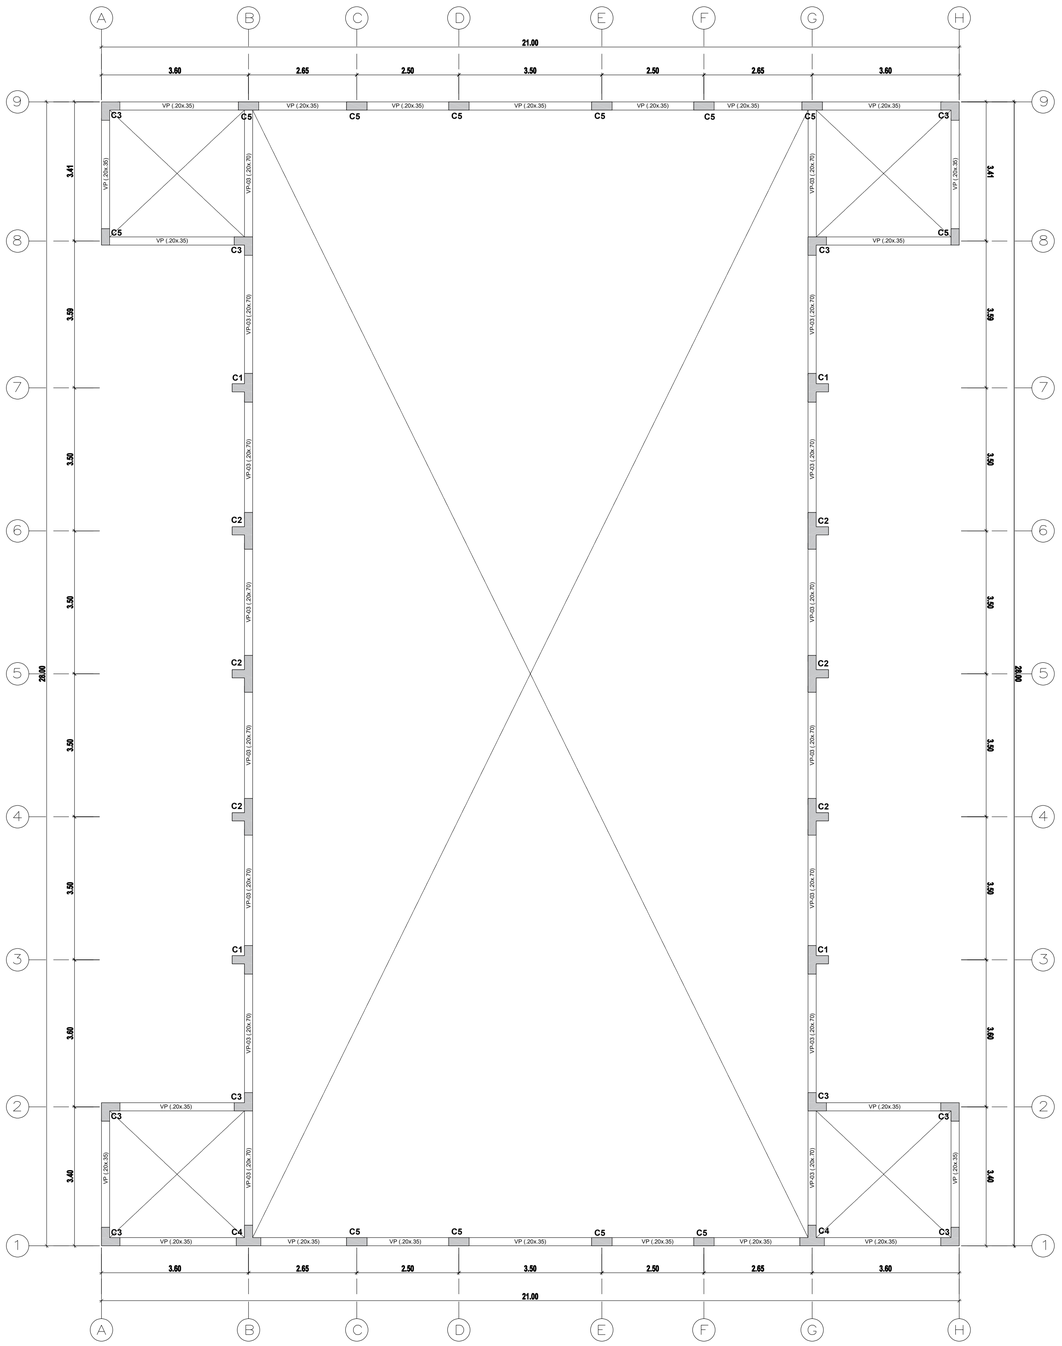


NPT +6.78
Esc=1/50

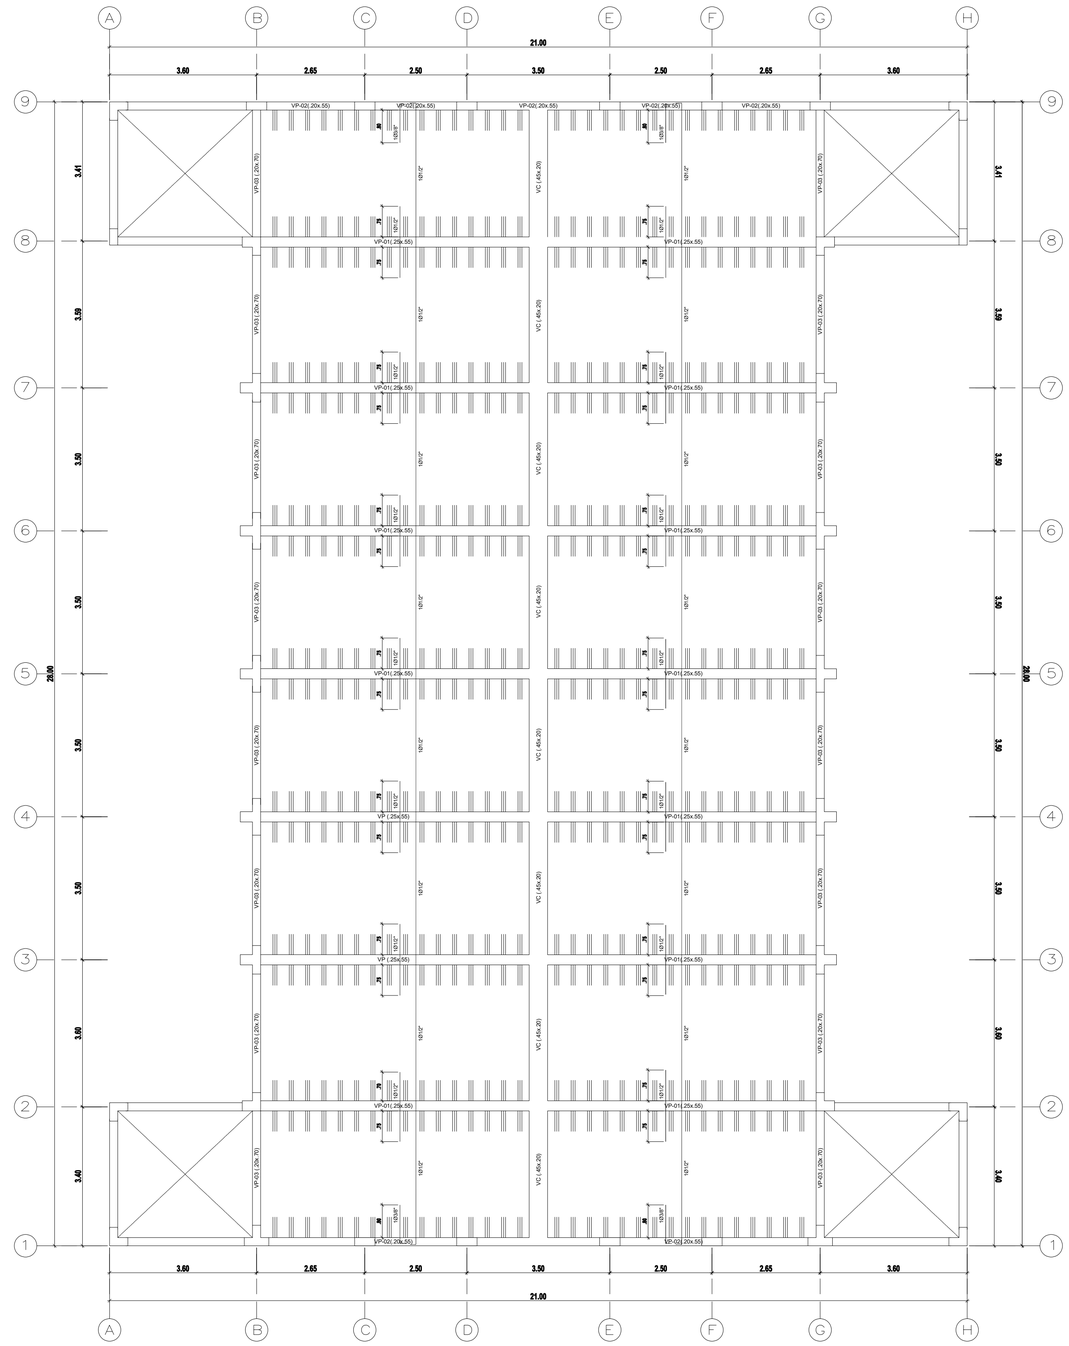

ALIGERADO - S/C = 100 kg/m2
Esc=1/50

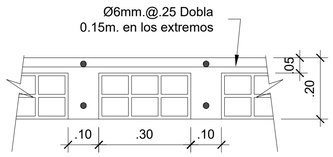


DETALLE ALIGERADO
H = 0.20 m.
Esc.=1/10

VC (0.45x0.20)




6ø3/8"
2 ø6mm: 1@.05;5@.10,R@.20
Esc.=1/25

VP-01(.25x.55)

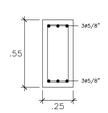


6ø5/8"
ø3/8": 1@.05;6@.10;R@.20
ESCALA : 1/25

VP-02(.20x.55)

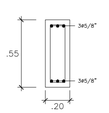


6ø5/8"
ø3/8": 1@.05;6@.10;R@.20
ESCALA : 1/25

VP-03 (.20x.70)

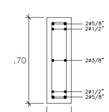

4ø5/8" + 4ø1/2" + 2ø3/8"
ø3/8": 1@.05;7@.10;R@.20
ESCALA : 1/25

VP-04(.20x.35)

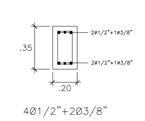

4ø1/2"+2ø3/8"
ø3/8": 1@.05;5@.10;R@.20
ESCALA : 1/25