AREA CONSTRUIDA

AREA POR CONSTRUIR

AREA POR CONSTRUIR

Campo de Fútbol	1 815m²
Área verde(Grass Natural)	821.66m²
Tribuna Polideportivo	170.41m²
Área de Vereda	323.24m²

CALLE DOS DE MAYO

CALLE LAS DUNAS

CALLE LOS TULIPANES

Ingreso peatonal

Ingreso para vehículos de emergencia

Contenedores para residuos sólidos

COCINA
N.P.T. -0.60
Congelador
Refrigerador

SUM
Auditorio/Comedor/Biblioteca
N.P.T. -0.60

SSHH
N.P.T. -0.65

SS.HH. ALUMNAS
N.P.T. -0.65

SS.HH. ALUMNOS
N.P.T. -0.65

SUM
DISCAPACITADOS
N.P.T. -0.65

SUM
DISCAPACITADOS
N.P.T. -0.65

N.P.T. -0.40

N.P.T. -0.30

N.P.T. -0.30

N.P.T. -0.10

PARAPETO DE CONCRETO

CISTERNA

ESTRADO
N.P.T. +0.80

JUEGOS INFANTILES

LABORATORIO DE QUÍMICA

Dirección
N.P.T. +0.00

Espera
N.P.T. +0.00

Coordinación Pedagógica
N.P.T. +0.00

T.S.
N.P.T. +0.00

SSHH
N.P.T. +0.00

Hall
N.P.T. +0.00

Sala de Profesores
N.P.T. +0.00

Psicología/Tutoría /Pastoral
N.P.T. +0.00

Entrevistas
N.P.T. +0.00

Secretaría
N.P.T. +0.00

Archivo/Servidor
N.P.T. +0.00

Inicial 3 Años
N.P.T. +0.00

Inicial 4 Años
N.P.T. +0.00

Inicial 5 Años
N.P.T. +0.00

1º Primaria
N.P.T. +0.00

SS.HH.

COPRODELI

PROYECTO :
I.E PÚBLICA DE GESTIÓN PRIVADA "COPRODELI SANTA CRUZ"

PLANO :
ARQUITECTURA - PLAN GENERAL PRIMER PISO

UBICACIÓN : Mz. O Sublote A Urb. Santa Cruz de Asia
Distrito: Asia Provincia: Cañete Departamento: Lima


PROFESIONAL : Arq. Félix Manuel Luna Núñez
CAP: 25486


DIBUJO :


ESCALA 1/125

FECHA: SETIEMBRE 2026


LAMINA : A-01

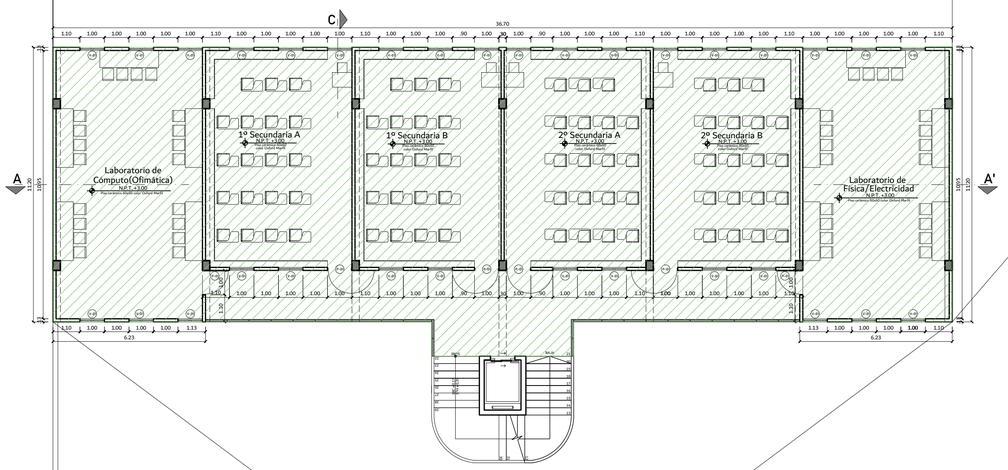

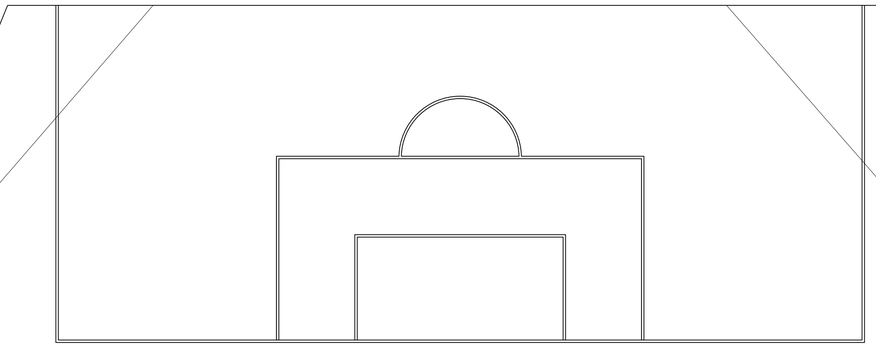

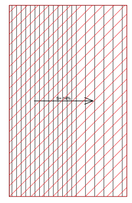



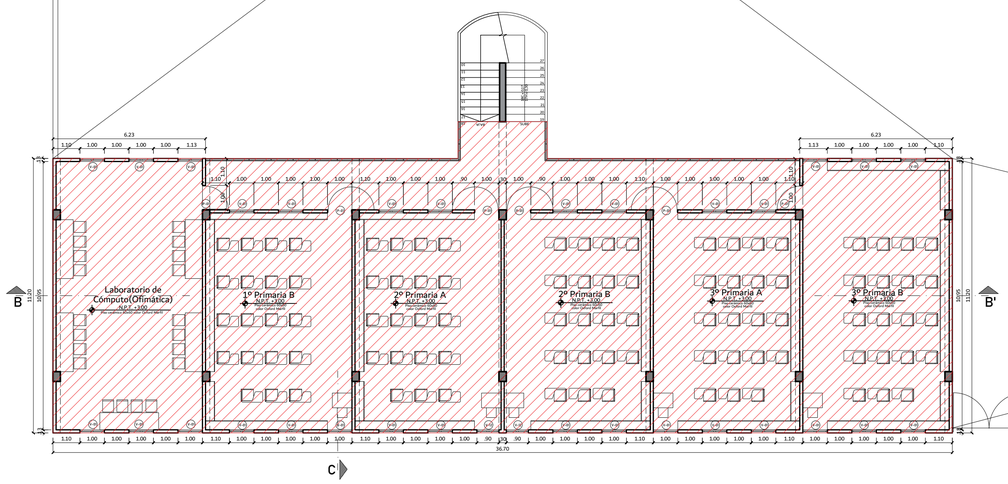

AREA CONSTRUIDA

AREA POR CONSTRUIR

AREA POR CONSTRUIR

2° Piso - Pabellón 2	419.16m²
Cobertura Polideportivo	895.89m²

COPRODELI

PROYECTO :
I.E PÚBLICA DE GESTIÓN PRIVADA "COPRODELI SANTA CRUZ"

PLANO :
ARQUITECTURA - PLAN GENERAL SEGUNDO PISO

UBICACIÓN : Mz. O Sublote A Urb. Santa Cruz de Asia
Distrito: Asia Provincia: Cañete Departamento: Lima


PROFESIONAL : Arq. Félix Manuel Luna Núñez
CAP: 25486


DIBUJO :

ESCALA 1/125

FECHA: SETIEMBRE 2026

LAMINA : A-02

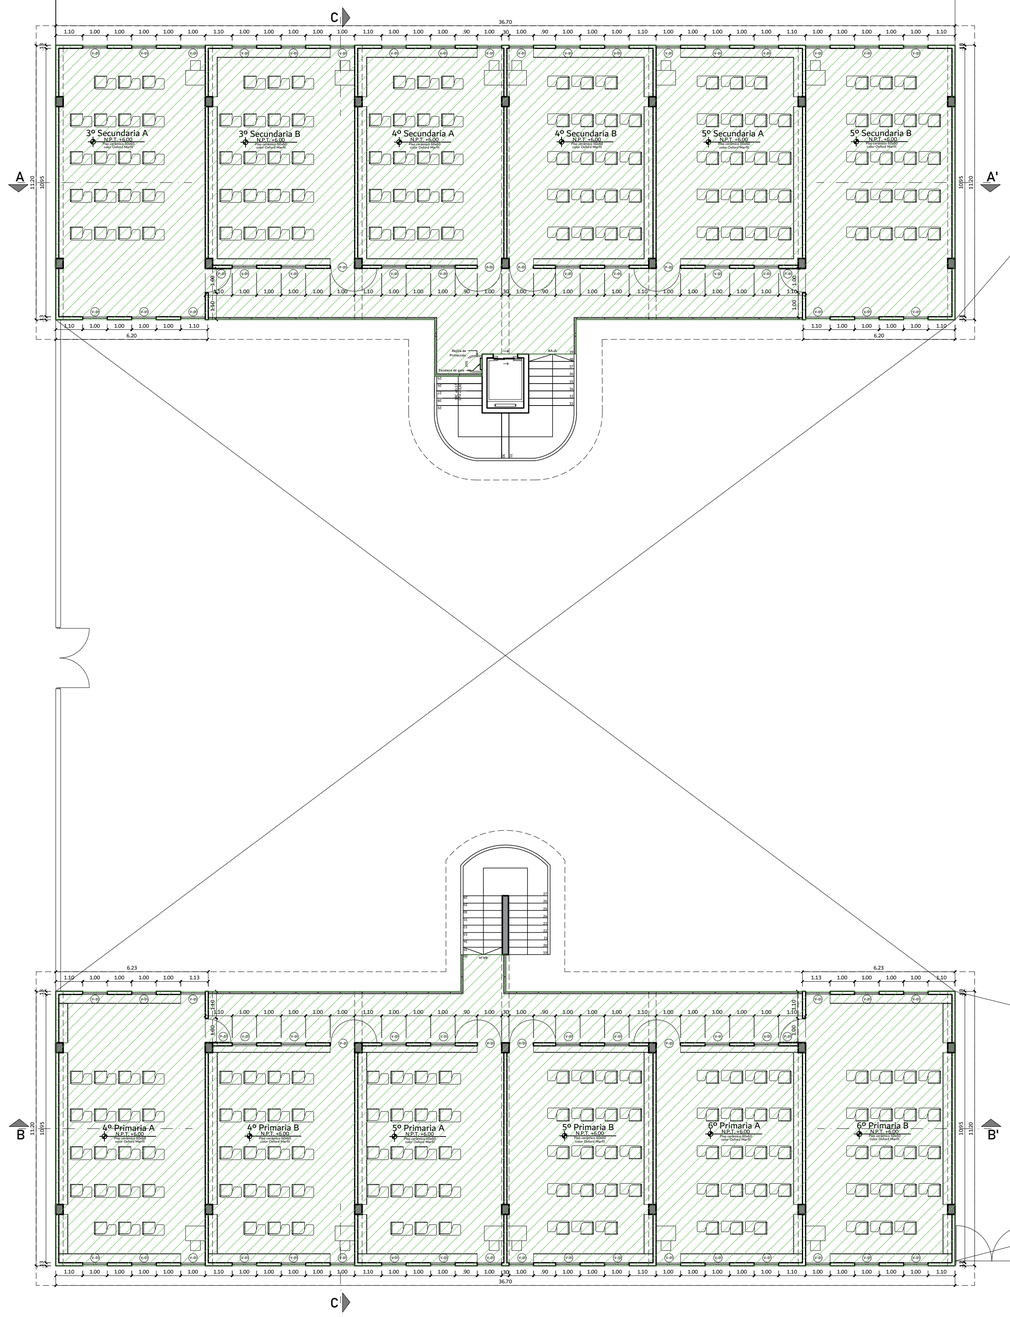

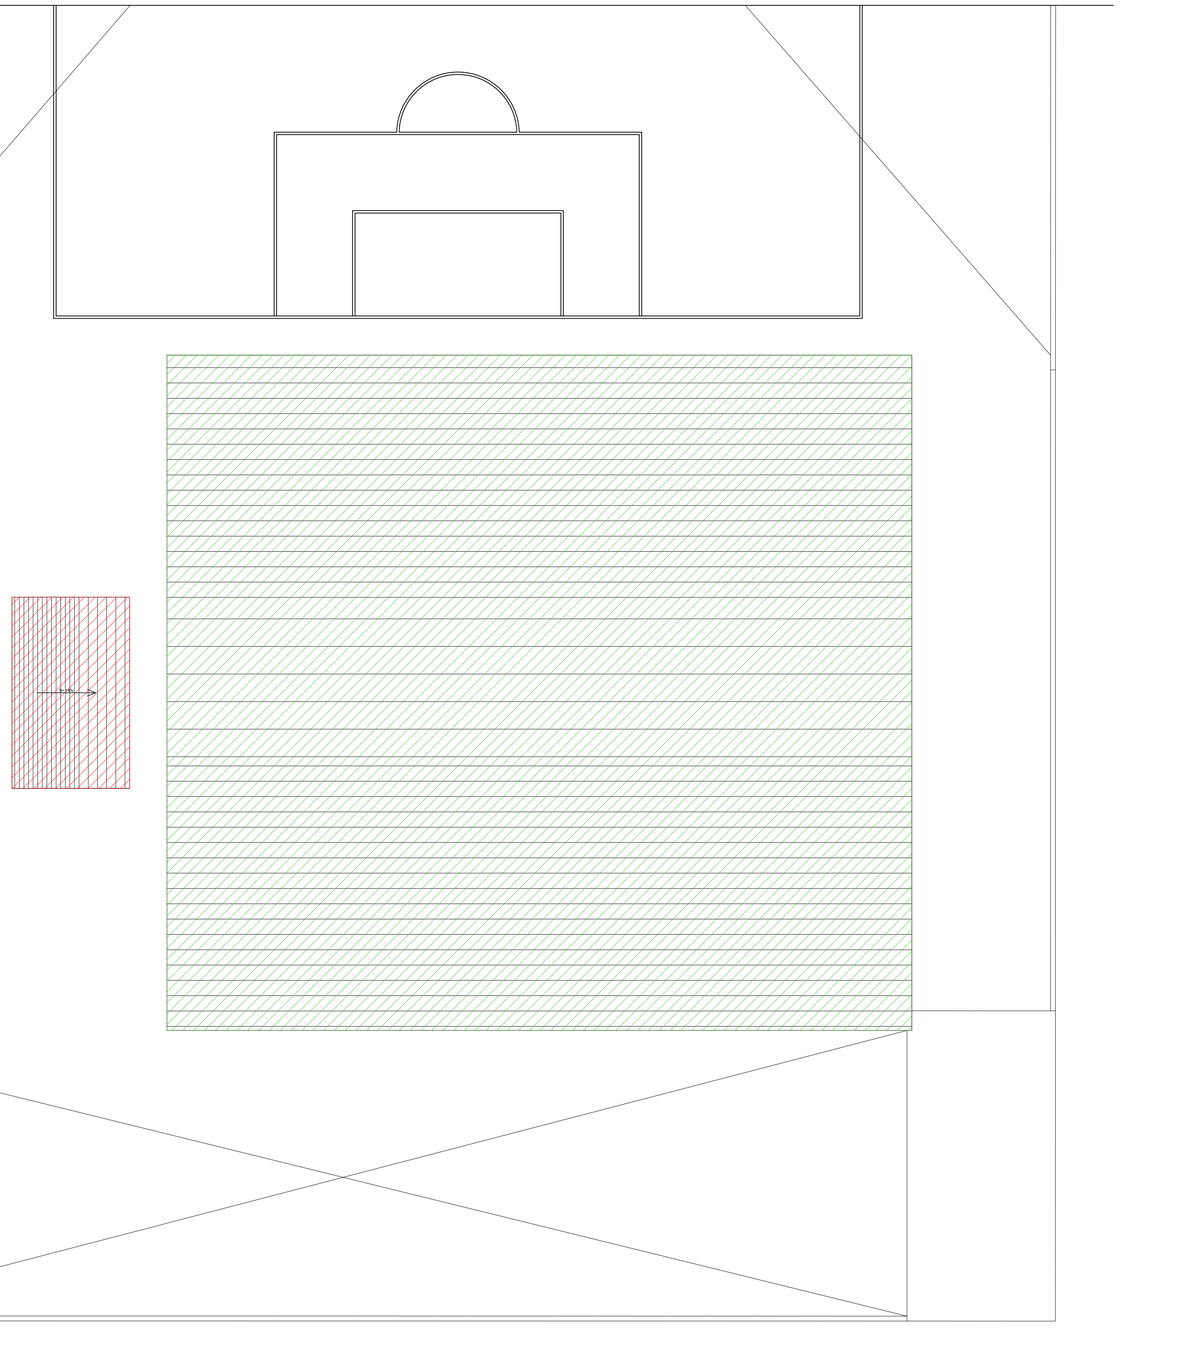

AREA POR CONSTRUIR

3º Piso - Pabellón 2	420.92m²
3º Piso - Pabellón 1	413.81m²
Cobertura Polideportivo	895.89m²

AREA CONSTRUIDA

AREA POR CONSTRUIR

COPRODELI

PROYECTO :
I.E PÚBLICA DE GESTIÓN PRIVADA
"COPRODELI SANTA CRUZ"

PLANO :
ARQUITECTURA - PLAN GENERAL TERCER PISO

UBICACIÓN : Mz. O Sublote A Urb. Santa Cruz de Asia
Distrito: Asia Provincia: Cañete Departamento: Lima


PROFESIONAL : Arq. Félix Manuel Luna Núñez
CAP: 25486


DIBUJO :

ESCALA 1/125


FECHA: SETIEMBRE 2026

LAMINA :
A-03

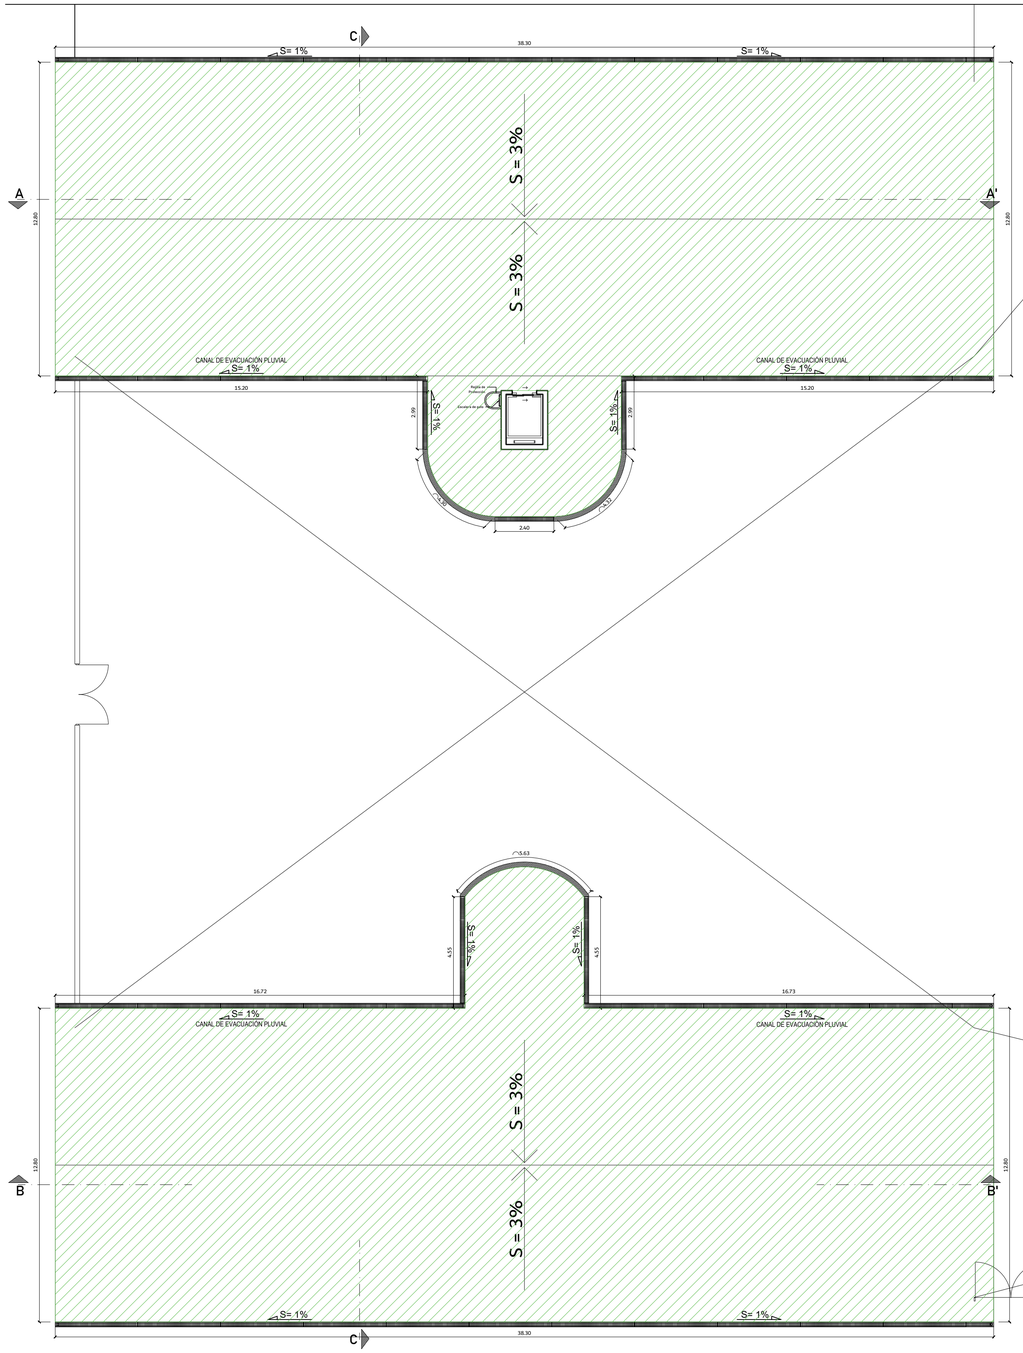

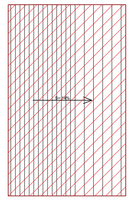



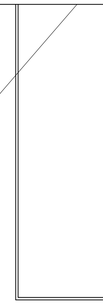

AREA POR CONSTRUIR

Techo - Pabellón 2	517.97m²
Techo - Pabellón 1	509.50m²
Cobertura Polideportivo	895.89m²

AREA CONSTRUIDA

AREA POR CONSTRUIR

COPRODELI

PROYECTO :
I.E PÚBLICA DE GESTIÓN PRIVADA
"COPRODELI SANTA CRUZ"

PLANO :
ARQUITECTURA - PLAN GENERAL TECHO

UBICACIÓN : Mz. O Sublote A Urb. Santa Cruz de Asia
Distrito: Asia Provincia: Cañete Departamento: Lima


PROFESIONAL : Arq. Félix Manuel Luna Núñez
CAP: 25486

DIBUJO :


ESCALA 1/125

FECHA: SETIEMBRE 2026


LAMINA :
A-04

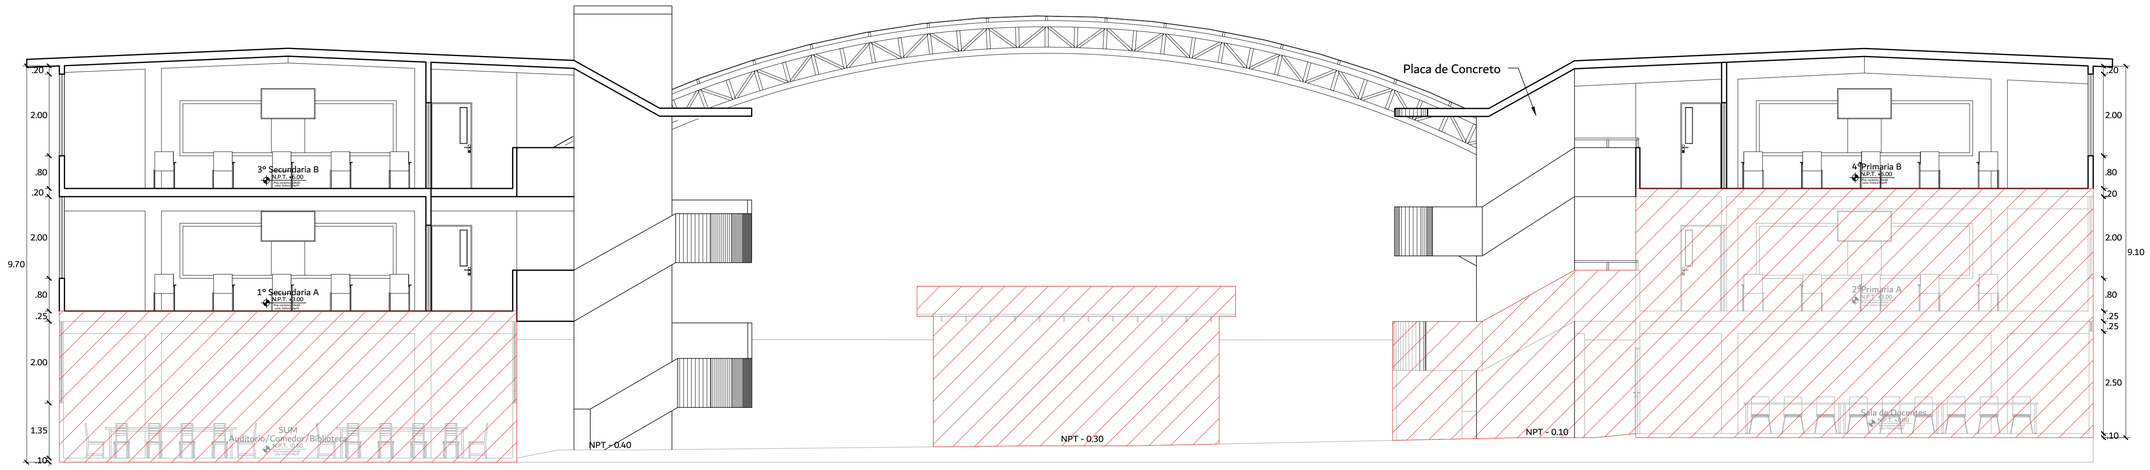

CORTE C-C
ESC:1/75

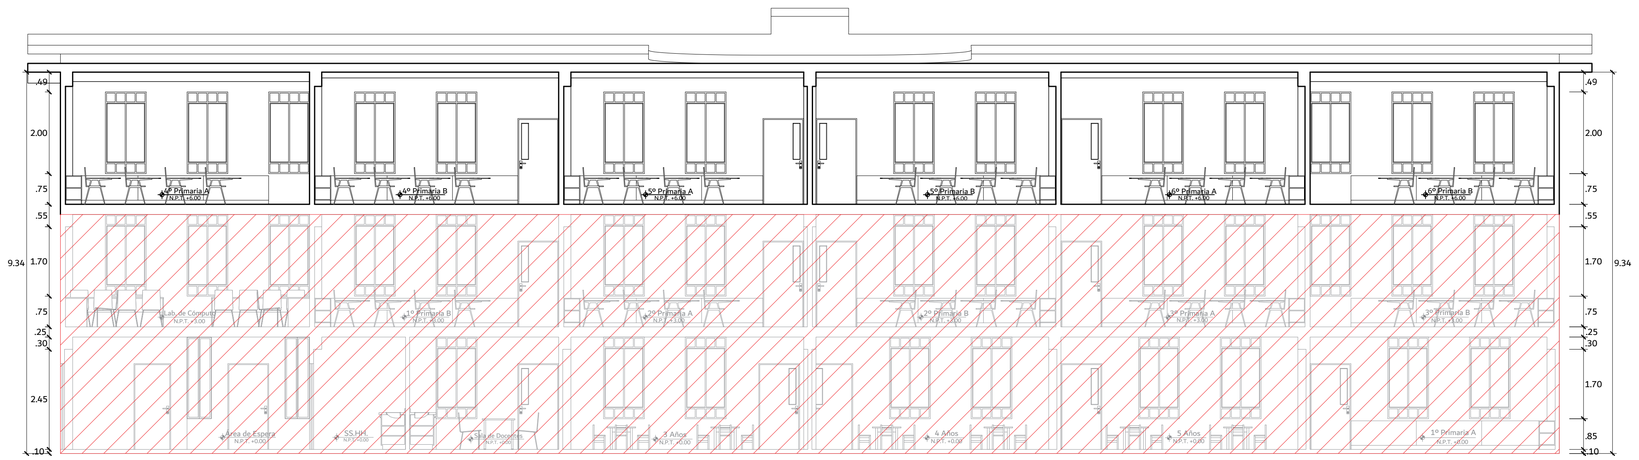

CORTE B-B
Esc: 1/75

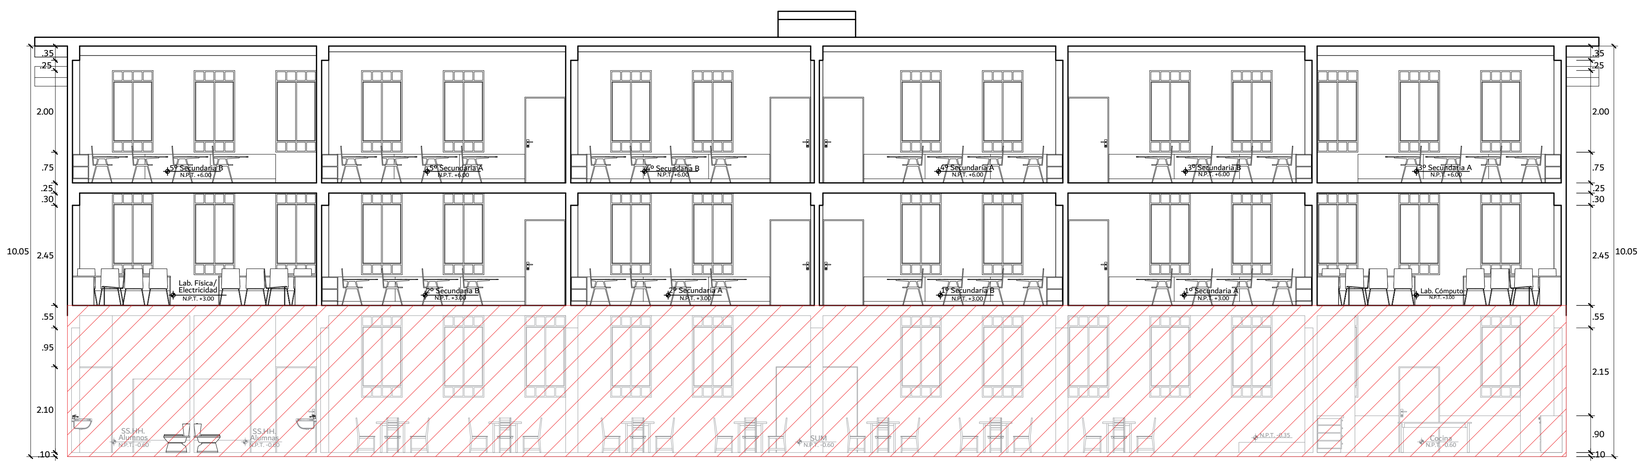

CORTE A-A
Esc: 1/75

AREA CONSTRUIDA

COPRODELI

PROYECTO :
I.E PÚBLICA DE GESTIÓN PRIVADA
"COPRODELI SANTA CRUZ"

PLANO :
ARQUITECTURA - CORTES

UBICACIÓN : Mz. Q Sublote A Urb. Santa Cruz de Asia
Distrito: Asia Provincia: Cañete Departamento: Lima

PROFESIONAL : Arq. Félix Manuel Luna Núñez
CAP: 25486

DIBUJO :

ESCALA 1/75

FECHA: SETIEMBRE 2026

LAMINA : A-05