ELEVACION POSTERIOR

A

B

B

CAMPO DE VOLEY

Contenedores para residuos sólidos

COCINA
N.P.T.: +0.00

N.P.T.: +0.15

SUM
Auditorio/Comedor/Biblioteca
N.P.T.: +0.00

SS.HH. ALUMNOS
N.P.T.: +0.00

SS.HH. ALUMNAS
N.P.T.: +0.00

SS.HH. DISCAPACITADOS
N.P.T.: +0.00

SS.HH. DISCAPACITADOS
N.P.T.: +0.00

ELEVACION LATERAL IZQUIERDA

ELEVACION LATERAL DERECHA

CAMPO DE FÚTBOL

ESTRADO

ESTACIONAMIENTO DE EMERGENCIA

ESTACIONAMIENTO DE EMERGENCIA

PARAPETO DE CONCRETO

Dirección
N.P.T.: +0.00

Coordinación Pedagógica y Bienestar
N.P.T.: +0.00

Área de Espera
N.P.T.: +0.00

SS.HH
N.P.T.: +0.00

Tópico
N.P.T.: +0.00

Secretaría
N.P.T.: +0.00

Archivo/Dep.
N.P.T.: +0.00

Sala de Reuniones
N.P.T.: +0.00

Sala de Docentes
N.P.T.: +0.00

Inicial 3 Años
N.P.T.: +0.00

Inicial 4 Años
N.P.T.: +0.00

Inicial 5 Años
N.P.T.: +0.00

1º Primaria A
N.P.T.: +0.00

SS.HH

SS.HH

SS.HH

SS.HH

C

C

PLANTA PRIMER PISO
Esc: 1/125

ELEVACION FRONTAL

A

AREA POR CONSTRUIR

Área verde	1,845.79m²
Campo de Voley	162.00m²

AREA CONSTRUIDA

AREA POR CONSTRUIR

COPRODELI

PROYECTO : INSTITUCION EDUCATIVA COPRODELI LA ASUNCION

PLANO : ARQUITECTURA- PLANTA GENERAL PRIMER PISO

UBICACIÓN : Urbanización Las Palmeras de San Fernando, Mz 87 Lote 3 Distrito: Ica Provincia: Ica Departamento: Ica

PROFESIONAL : Arq. Félix Manuel Luna Nuñez CAP 25486

DIBUJO :


ESCALA 1/125

FECHA : SETIEMBRE 2026

LAMINA : A-01

01 de 17

ELEVACION POSTERIOR

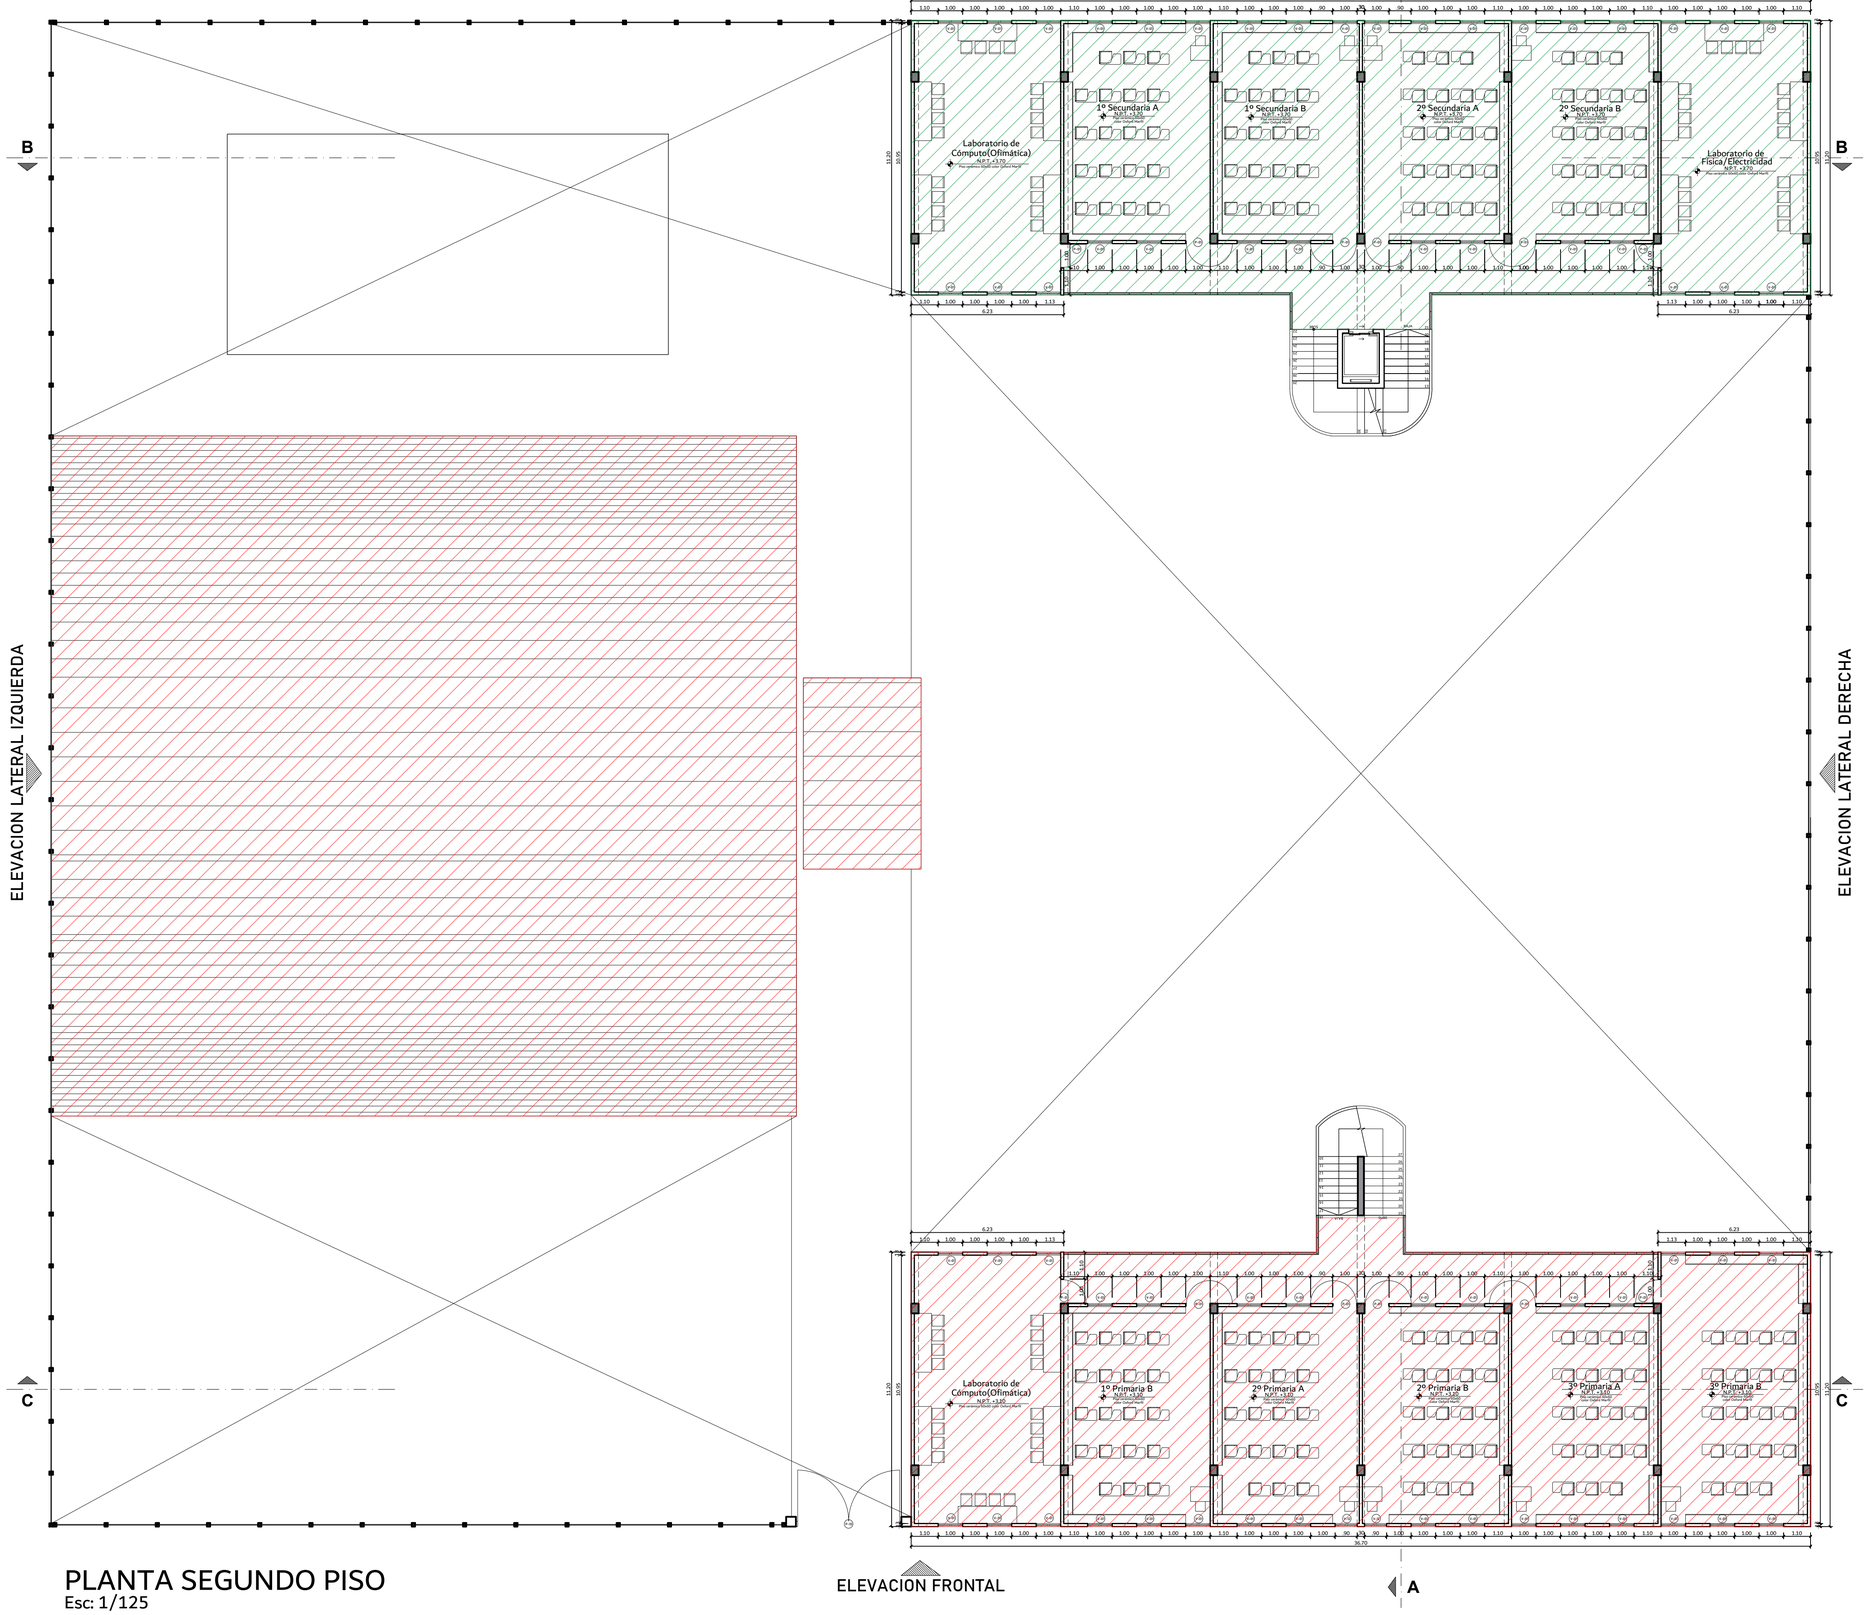

ELEVACION LATERAL IZQUIERDA

ELEVACION LATERAL DERECHA

ELEVACION FRONTAL

AREA POR CONSTRUIR

Pabellón 2 - 2 Piso	419.16m²

AREA CONSTRUIDA

AREA POR CONSTRUIR


PLANTA SEGUNDO PISO

Esc: 1/125

COPRODELI

PROYECTO : INSTITUCION EDUCATIVA COPRODELI LA ASUNCION			
PLANO : ARQUITECTURA- PLANTA GENERAL SEGUNDO PISO			
UBICACIÓN : Urbanización Las Palmeras de San Fernando, Mz 87 Lote 3 Distrito: Ica Provincia: Ica Departamento: Ica			LAMINA : A-02
PROFESIONAL : Arq. Félix Manuel Luna Nuñez CAP 25486			
DIBUJO :	ESCALA 1/125	FECHA : SETIEMBRE 2026	

ELEVACION POSTERIOR

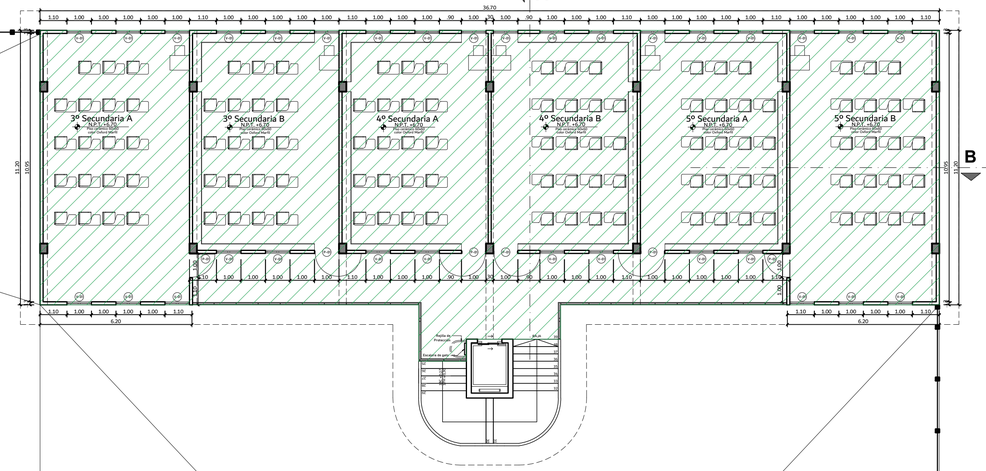


ELEVACION LATERAL IZQUIERDA



ELEVACION LATERAL DERECHA



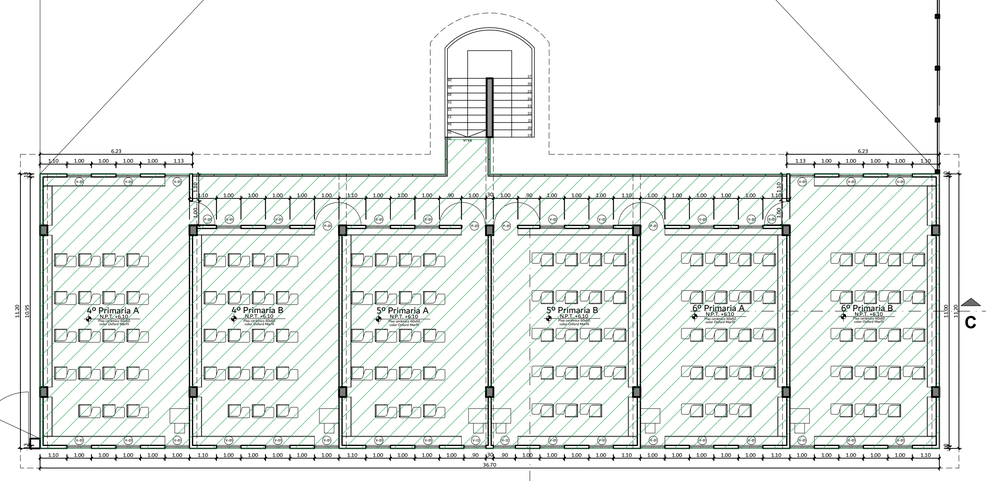

ELEVACION FRONTAL

A

AREA POR CONSTRUIR

Pabellón 2 - 3 Piso	420.92m²
Pabellón 1 - 3 Piso	413.63m²

AREA CONSTRUIDA

AREA POR CONSTRUIR

PLANTA TERCER PISO

Esc: 1/125

COPRODELI

PROYECTO : INSTITUCION EDUCATIVA COPRODELI LA ASUNCION

PLANO : ARQUITECTURA- PLANTA GENERAL TERCER PISO

UBICACIÓN : Urbanización Las Palmeras de San Fernando, Mz 87 Lote 3 Distrito: Ica Provincia: Ica Departamento: Ica


PROFESIONAL : Arq. Félix Manuel Luna Nuñez CAP 25486

DIBUJO :

ESCALA 1/125

FECHA : SETIEMBRE 2026

LAMINA : A-03

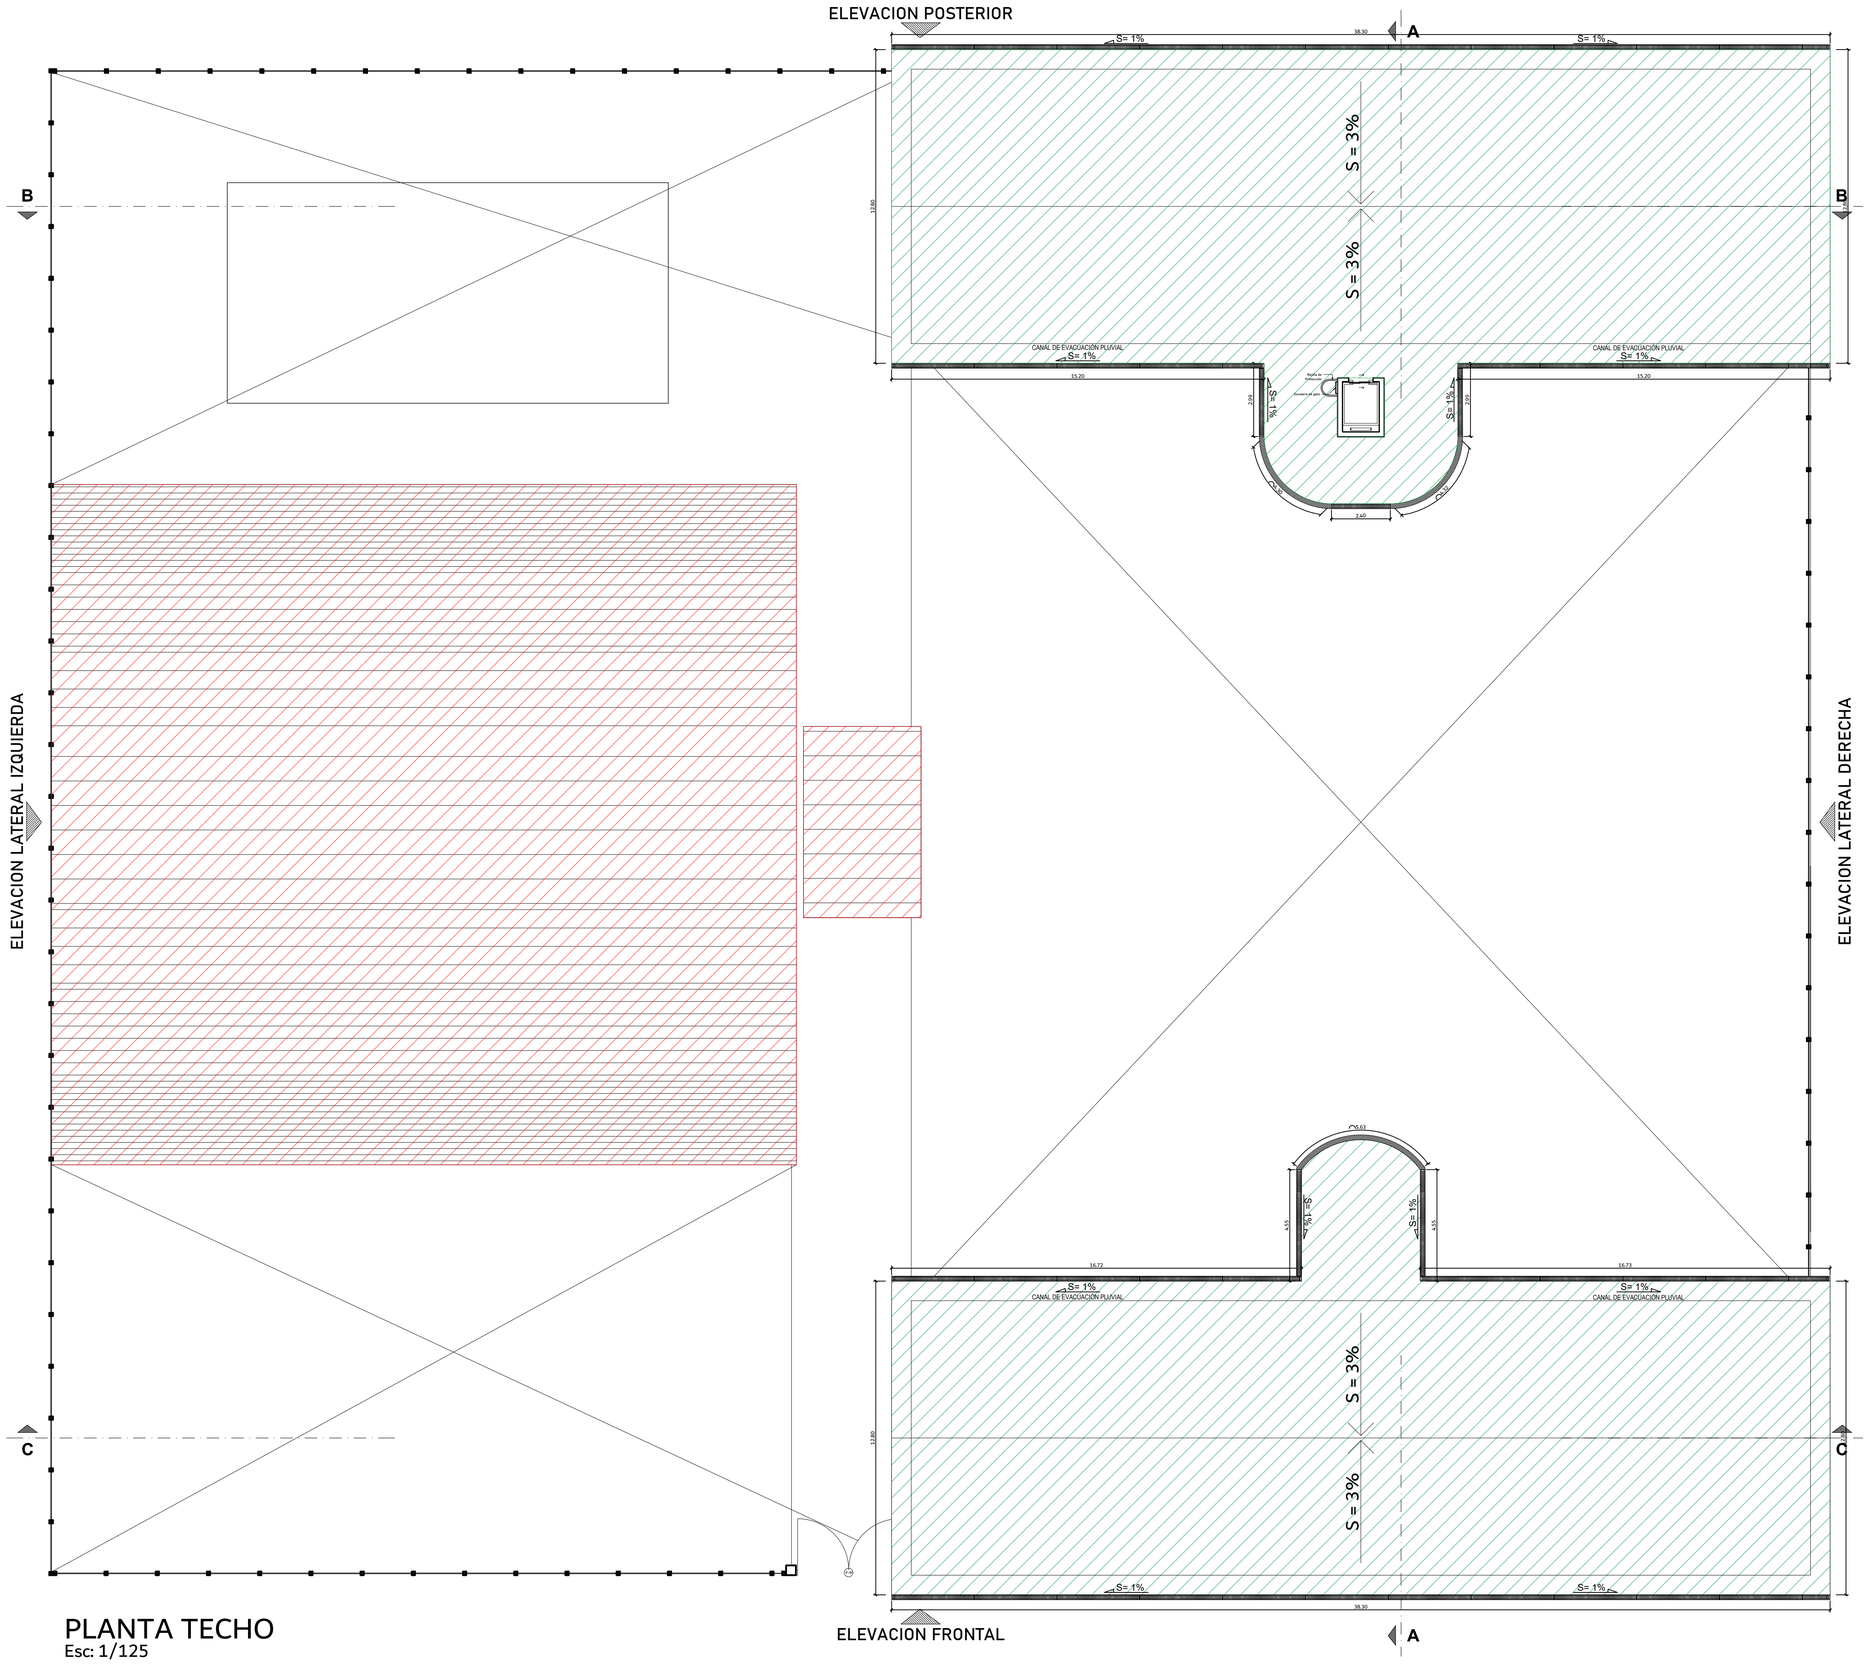

PLANTA TECHO

Esc: 1/125

AREA POR CONSTRUIR


Pabellón 2 - Techo	527.70m²
Pabellón 1 - Techo	516.43m²

AREA CONSTRUIDA


AREA POR CONSTRUIR

COPRODELI


PROYECTO : INSTITUCION EDUCATIVA COPRODELI LA ASUNCION			
PLANO : ARQUITECTURA- PLANTA TECHO			
UBICACIÓN : Urbanización Las Palmeras de San Fernando, Mz 87 Lote 3 Distrito: Ica Provincia: Ica Departamento: Ica			LAMINA : A-04
PROFESIONAL : Arq. Félix Manuel Luna Nuñez CAP 25486			
DIBUJO :	ESCALA 1/125	FECHA : SETIEMBRE 2026	

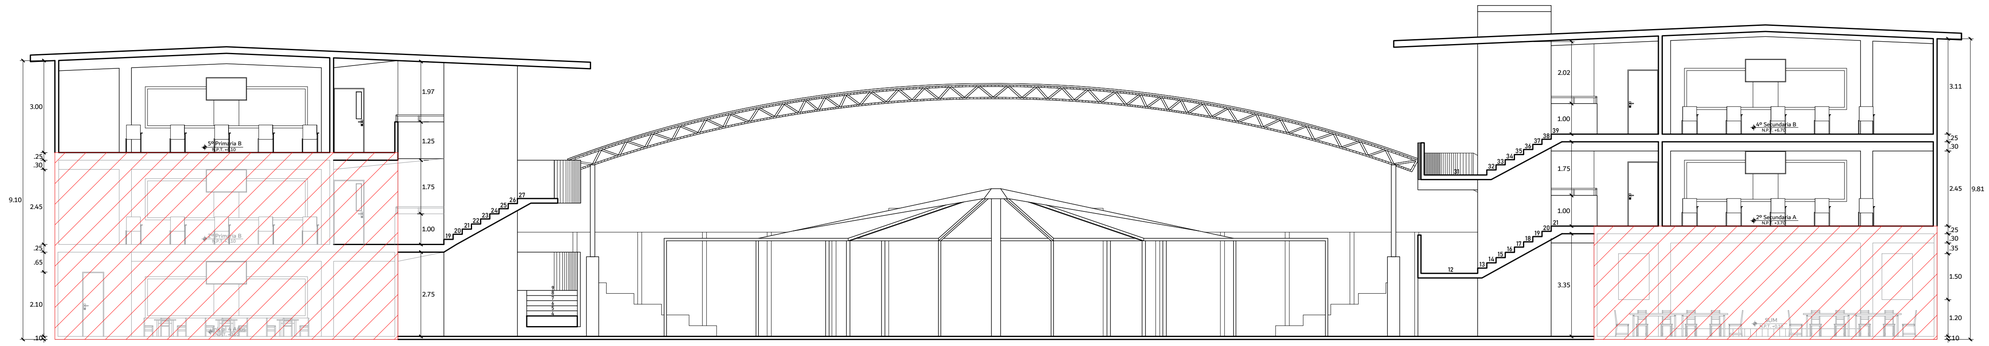

CORTE A-A
Esc: 1/100

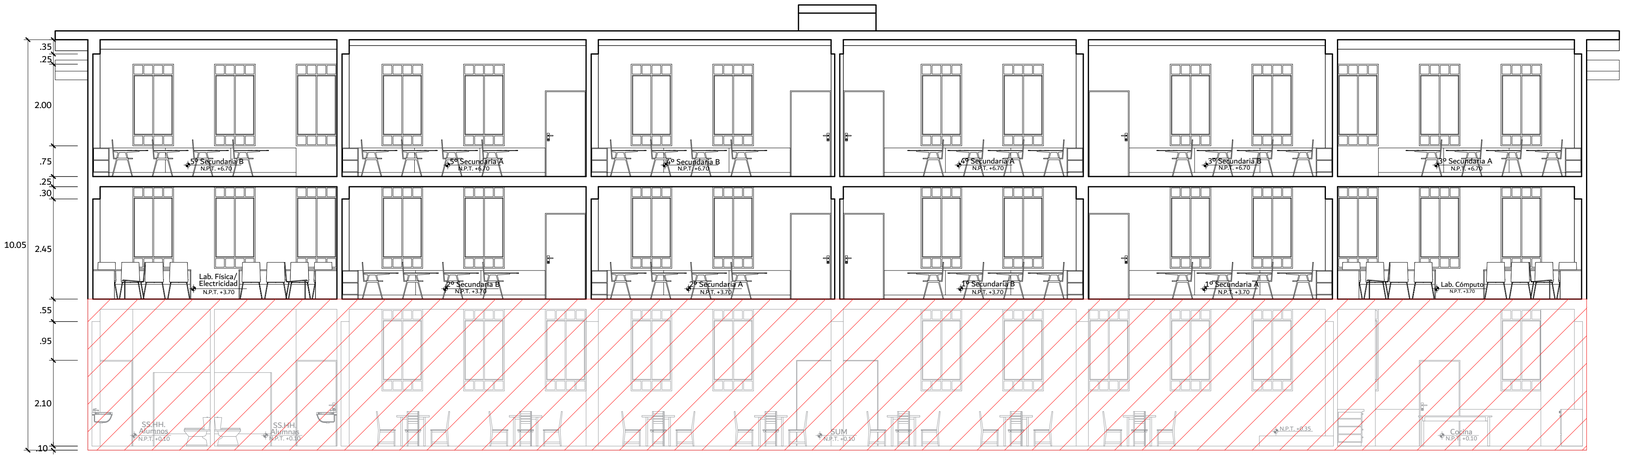

CORTE B-B
Esc: 1/75

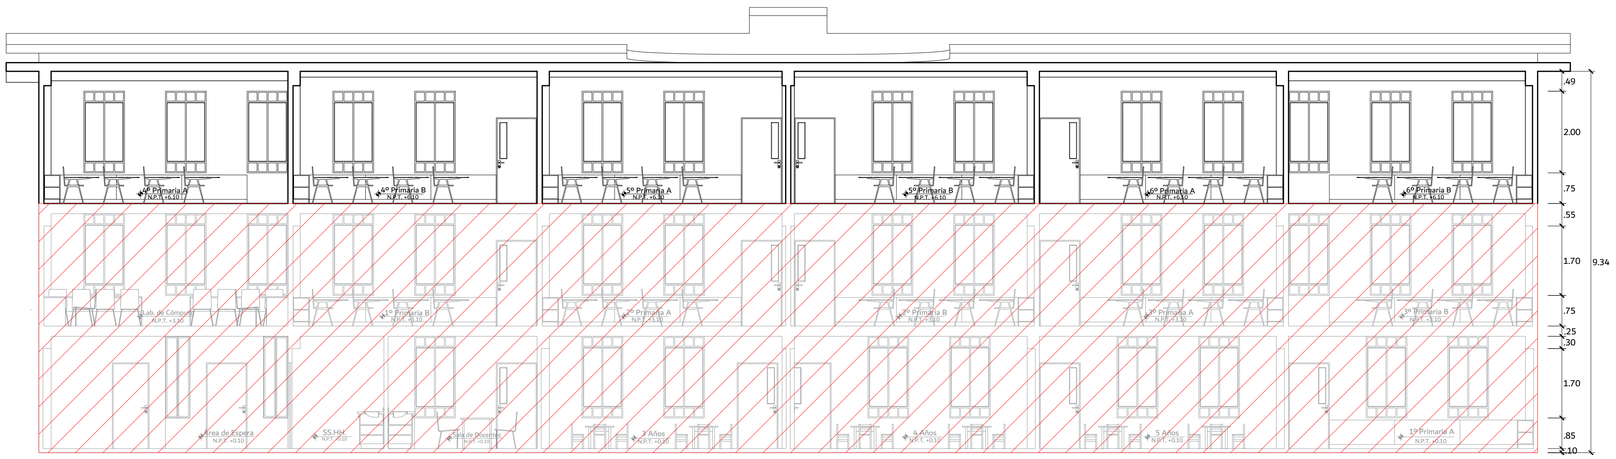

CORTE C-C
Esc: 1/75

AREA CONSTRUIDA

COPRODELI

PROYECTO :
INSTITUCION EDUCATIVA COPRODELI LA ASUNCION

PLANO :
ARQUITECTURA- CORTES

UBICACIÓN : Urbanización Las Palmeras de San Fernando, Mz 87 Lote 3
Distrito: Ica Provincia: Ica Departamento: Ica

PROFESIONAL : Arq. Félix Manuel Luna Nuñez
CAP 25486

DIBUJO :

ESCALA Indicada

FECHA : SETIEMBRE 2026

LAMINA : A-05